


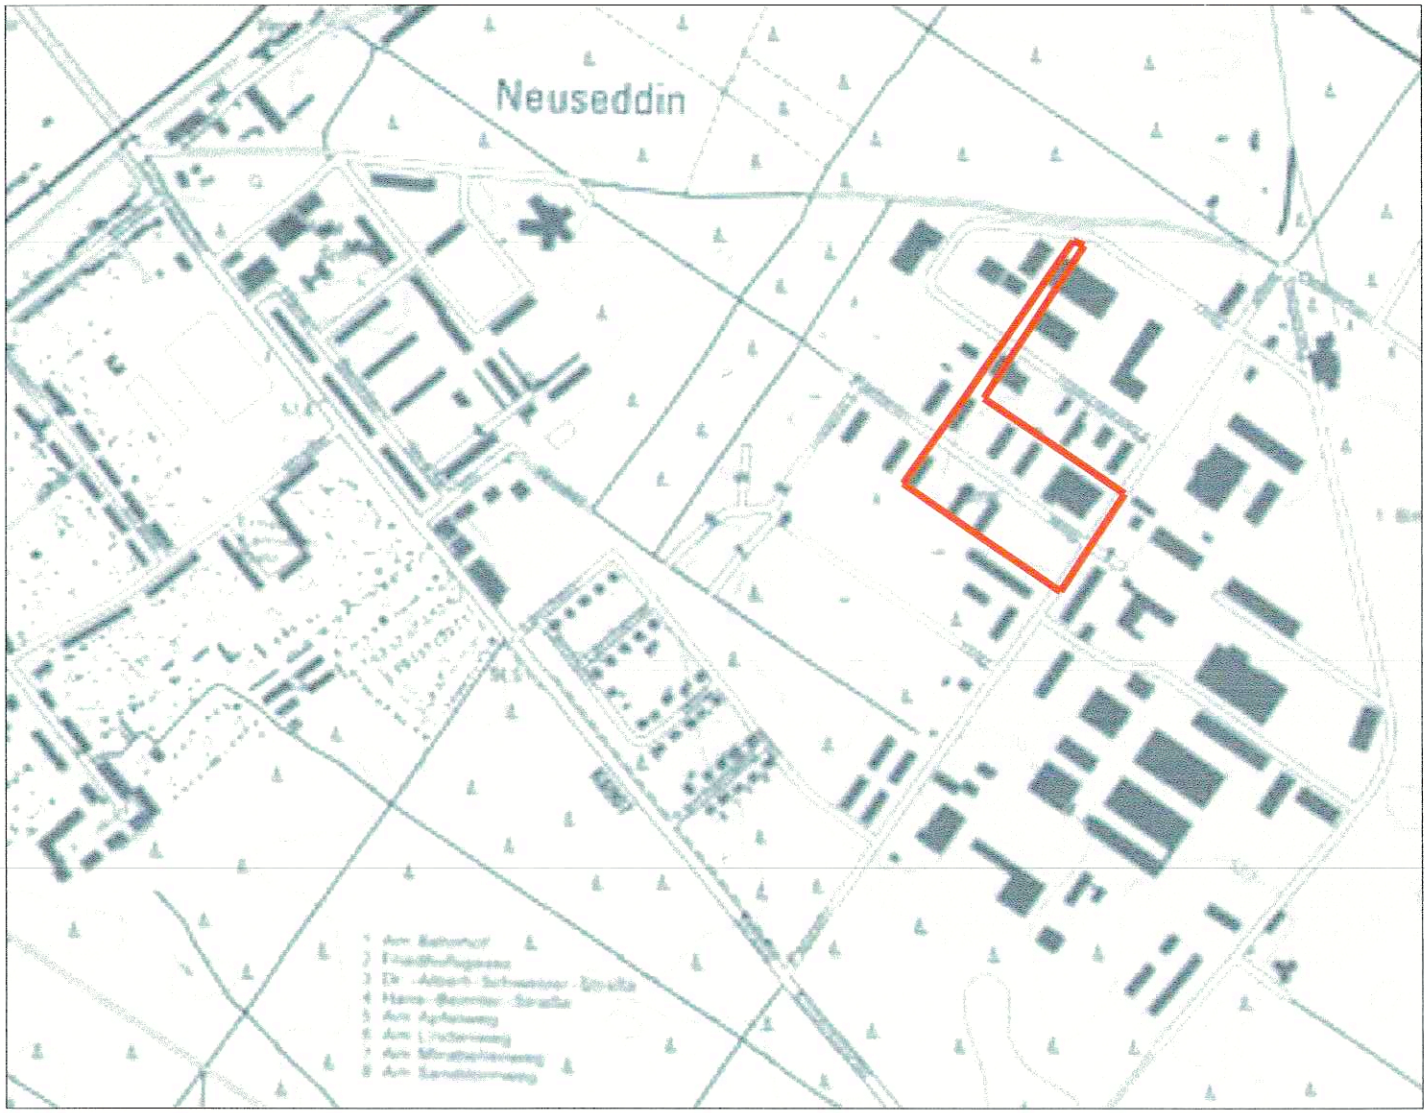

Textliche Festsetzungen

- In den Gewerbegebieten sind die in § 8 Abs. 2 Nr. 1 und Nr. 3 der BauNVO genannten Tankstellen und Vergnügungsstätten nicht zulässig.
- In den Gewerbegebieten sind notwendige technische Aufbauten, wie z. B. Aufzugsschächte ausnahmsweise bis zu einer Höhe von 3,0 m über der festgesetzten Traufhöhe zulässig. Die Festsetzung gilt nicht für Schornsteine und Lüftungsrohre, wenn diese nach anderen Vorschriften höher sein müssen. Die nach anderen Vorschriften erforderliche Höhe darf nicht überschritten werden.
- Auf den Baugrundstücken ist eine Befestigung von Stellplätzen, Zufahrten und Wegen wasser- und luftdurchlässig (z. B. Großpflaster mit hohem Fugenanteil, wassergebundene Decke, Schotterrasen, Rasengittersteine) herzustellen. Wasser- und Luftdurchlässigkeit mindernde Befestigungen wie Betonunterbau, Fugenverguss oder Asphaltierungen sind unzulässig.
- In den Gewerbegebieten GE I und GE II sind auf den Teilflächen 1-5 nur Betriebe und Anlagen zulässig, deren Lärmemissionen soweit begrenzt sind, dass die in der folgenden Tabelle angegebenen Emissionskontingente LEK nach DIN 45691:2006-12, "Geräuschkontingentierung" weder tags (6:00-22:00) noch nachts (22:00-6:00) überschritten werden:

Teilfläche	Abgrenzung	LEK, tags in dB/m²	LEK,nachts in dB/m²
1	BCDEB	52	30
2	EDGFE	56	42
3	FGHJKF	64	50
4	LMNOL	56	35
5	NOPQN	58	45


Die Prüfung der Einhaltung erfolgt nach DIN 45691:2006-12, Abschnitt 5.

- In den Gewerbegebieten sind an- und abschwellende Werbeanlagen (d.h. größer und kleiner werdende Leuchtreklamen) unzulässig.
- Die Einteilung der Straßenverkehrsfläche ist nicht Bestandteil der Festsetzungen.
- Im Geltungsbereich dieses Bebauungsplans treten alle bisherigen Festsetzungen und baurechtlichen Vorschriften, die verbindliche Regelungen der in § 9 Abs. 1 des Baugesetzbuchs bezeichneten Art enthalten, außer Kraft.

Hinweise

Die der Planung zugrunde liegenden Vorschriften (Gesetze, Verordnungen, Erlasse und DIN-Vorschriften) können bei der Gemeindeverwaltung Seddiner See, Kiefernweg 5, 14554 Seddiner See eingesehen werden.

Baufeldfreimachungen und der Beginn von Bauarbeiten sind außerhalb der Brutzeiten zwischen 1. Oktober und 28. Februar durchzuführen. Sollten bauvorbereitende Maßnahmen und grundlegende, flächeneingreifende Bauaktivitäten innerhalb dieser Zeit beginnen bzw. sich bis in die Brutzeit hinziehen, wird eine ökologische Baubegleitung empfohlen, um bei spontanen Ansiedlungen von Brutvögeln rechtzeitig geeignete Maßnahmen zur Vermeidung von artenschutzrechtlichen Verboten ergreifen zu können.

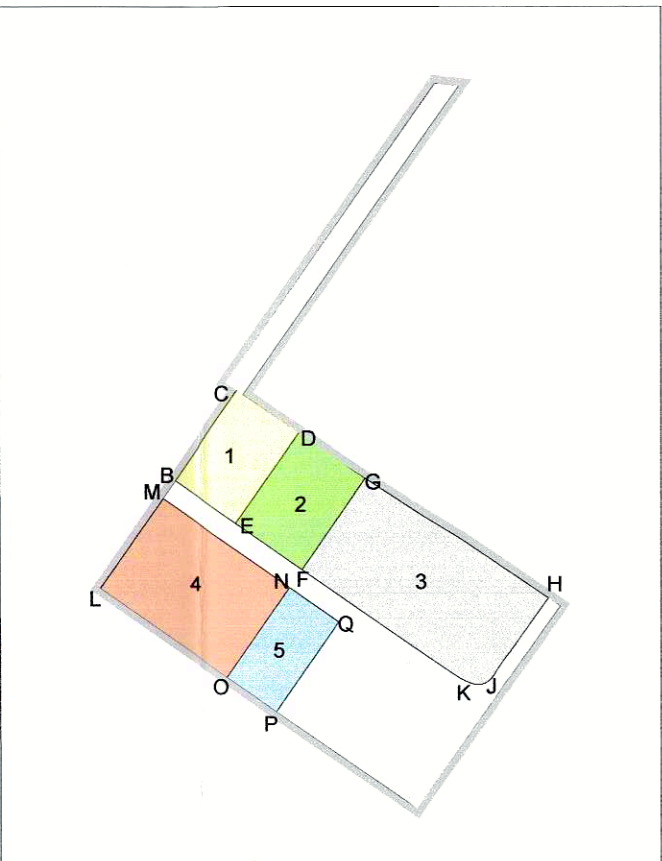

Nebenzeichnung 1
Geräuschkontingentierung zur Textlichen Festsetzung Nr. 4
Maßstab 1:4.000

Verfahrensvermerke

Die Gemeindevertretung Seddiner See hat in ihrer Sitzung am 27.09.2011 die Aufstellung des Bebauungsplanes "Kiefernweg" gem. § 13a BauGB beschlossen.

Seddiner See, den 29.01.2013

Der Bürgermeister

Die verwendete Planunterlage enthält den Inhalt des Liegenschaftskatasters mit Stand vom 20.12.2012 und weist die planungsrelevanten baulichen Anlagen sowie Straßen, Wege und Plätze vollständig nach. Sie ist hinsichtlich der planungsrelevanten Bestandteile geometrisch einwandfrei. Die Übertragbarkeit der neuzubildenden Grenzen in die Örtlichkeit ist einwandfrei möglich.

Datum: 28.01.2013

Öffentlich bestellte Vermessungsingenieurin

Die Gemeindevertretung Seddiner See hat in ihrer Sitzung am 25.09.2012 die Teilung des Geltungsbereiches des Bebauungsplanes "Kiefernweg" beschlossen. Das Verfahren wird als Bebauungsplan "Kiefernweg Teil I - Gewerbegebiet" und "Kiefernweg Teil II - Wohngebiet" fortgeführt. Der Teilungsbeschluss ist im Amtsblatt Nr. 11/2012 vom 30.10.2012 öffentlich bekannt gemacht worden.

Seddiner See, den 28.01.2013

Der Bürgermeister

Der Entwurf des Bebauungsplanes mit Begründung wurde in der Zeit vom 8.11.2012 bis zum 10.12.2012, montags, mittwochs und donnerstags von 9-12 Uhr und 13-15 Uhr, dienstags von 9-12 Uhr und 14-18 Uhr und freitags von 9-12 Uhr in der Gemeindeverwaltung gem. § 3 Abs. 2 BauGB öffentlich ausgelegt. Die Auslegung wurde im Amtsblatt Nr. 11/2012 vom 30.10.2012 bekannt gemacht.

Seddiner See, den 29.01.2013

Der Bürgermeister

Die Gemeindevertretung hat den Bebauungsplan nach Prüfung der Stellungnahmen der Träger öffentlicher Belange und der Anregungen gem. § 3 Abs. 2 BauGB in ihrer Sitzung am 15.01.2013 als Sitzung beschlossen.

Seddiner See, den 29.01.2013

Der Bürgermeister

Die Satzung des Bebauungsplanes wird hiermit ausgefertigt.

Seddiner See, den 29.01.2013

Der Bürgermeister

Der Bebauungsplan ist gem. § 10 Abs. 3 BauGB mit der Veröffentlichung im Amtsblatt 1/2013 vom 30.01.2013 in Kraft getreten. Auf die Frist für die Geltendmachung einer Verletzung von Verfahrens- und Formvorschriften und auf die Vorschriften des § 44 BauGB wurde hingewiesen. Jedermann kann den Bebauungsplan einsehen und über den Inhalt Auskunft erhalten.


Seddiner See, den 31.01.2013

Der Bürgermeister



Gemeinde Seddiner See

Bebauungsplan "Kiefernweg Teil I - Gewerbegebiet"

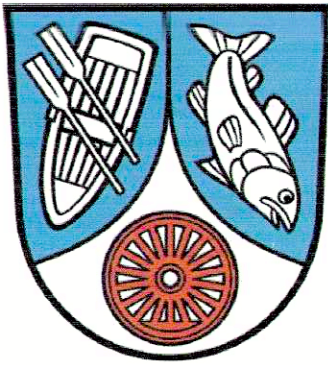

für die Flurstücke 50/77 teilweise, 50/78 teilweise, 50/80 teilweise, 50/83 teilweise, 50/84 teilweise, 50/94 teilweise, 50/95, 50/106 teilweise, 295, 375, 377, 422, 436 der Flur 2 Gemarkung Neuseddin in der Gemeinde Seddiner See im Ortsteil Neuseddin

Zeichenerklärung

Art und Maß der baulichen Nutzung, Bauweise

Gewerbegebiet (§ 8 BauNVO)

GE

Zahl der Vollgeschosse als Höchstmaß (§ 16 BauNVO)

II

Grundflächenzahl (§16 BauNVO)

GRZ 0,25

Geschossflächenzahl (§ 16 BauNVO)

0,5

Traufhöhe über festgesetzter Oberkante

TH 7,50 m

Baugrenze (§ 23 BauNVO)

Verkehrsflächen

Öffentliche Straßenverkehrsfläche (§ 9 Abs. 1 Nr. 11 BauGB)



Straßenverkehrsfläche besondere Zwecksbestimmung "Öffentlicher Parkplatz" (§ 9 Abs. 1 Nr. 11 BauGB)



Straßenbegrenzungslinie (§ 9 Abs. 1 Nr. 11 BauGB)



Höhenpunkt Oberkante Gehweg

OK 55,00 m über NHN

Grünflächen

Umgrenzung von Flächen zum Erhalt von Bäumen, Sträuchern und sonstigen Bepflanzungen (§ 9 Abs. 1 Nr. 25 BauGB)



Sonstige Festsetzungen

Geltungsbereichsgrenze (§ 9 Abs. 7 BauGB)



Abgrenzung unterschiedlicher Nutzungsmaße (§ 16 Abs. 5 BauNVO)



Planunterlage

vorhandene Bebauung



Flurstücksgrenze



Flurstücksnummer, Hausnummer



Bestandsbaum



Plangrundlage: Die Vermessung basiert auf dem Höhensystem des Deutschen Haupthöhennetzes 1992 (DHHN 92).

Gemeinde Seddiner See

Bebauungsplan "Kiefernweg Teil I - Gewerbegebiet"

Auftraggeber:

Auftragnehmer:

Gemeinde Seddiner See
Kiefernweg 5
14554 Seddiner See

Jahn, Mack & Partner
Alt-Moabit 73
10555 Berlin

Maßstab 1:1000

