

Planteil (Teil A)

Planzeichnung  
1 : 500

Nutzungsschablone:

|                       |                         |
|-----------------------|-------------------------|
| Art der baul. Nutzung | Zahl der Vollgeschosse  |
| GRZ                   |                         |
| Bauweise              | Dachform<br>Dachneigung |




Liegenschaftskarte des Kataster- und Vermessungsamtes  
Grundlage erstellt am 15.11.2013  
Vermessungsbüro Dipl.-Ing. Obermann  
An der Bahn 2  
16547 Birkenwerder

Aufnahme: November 2013  
Plangebiet: Kreis Potsdam-Mittelmark  
Gemarkung Seddin  
Flur 2  
Flurstücke (alt) 496, Flurstücke (neu) 654, 656, 664, 665, 666, 668, 674, 675, 676, 677  
Flur 2  
Teilflurstücke 58, 495  
Höhenbezug: DHNN, 92 ü. NHN ist ca. NN  
Maßstab: 1:500

Textteil (Teil B)

1. RECHTSGRUNDLAGEN  
Baugesetzbuch (BauGB)  
in der Fassung der Bekanntmachung vom 23.09.2004 (BGBl. S.2414), zuletzt geändert durch Gesetz vom 20.11.2014 (BGBl. S.1748)  
Verordnung über die bauliche Nutzung der Grundstücke (BauNutzungsverordnung – BauNVO)  
Neufassung vom 23.01.1990 (BGBl. S.132), zuletzt geändert durch Artikel 2 des Gesetzes vom 11.06.2013 (BGBl. S.1548).  
Verordnung über die Ausarbeitung der Bauleitpläne und die Darstellung des Planinhaltes (Planzeichenverordnung – PlanZV 90)  
Fassung vom 18.12.1990 (BGBl. 1991, S.58), zuletzt geändert durch Artikel 2 des Gesetzes vom 22.07.2011 (BGBl. S.1509).  
Brandenburgische Bauordnung (BbgBO)  
vom 17.09.2008 (GVBl./08, [Nr.14] S.226), zuletzt geändert durch Artikel 2 des Gesetzes vom 29.11.2010 (GVBl./10, Nr.39)  
Gesetz über Naturschutz und Landschaftspflege (Bundesnaturschutzgesetz – BNatSchG)  
vom 29.07.2009 (BGBl. S.2542), zuletzt geändert durch Artikel 4 Abs.100 des Gesetzes vom 07.08.2013 (BGBl. / S.3154)

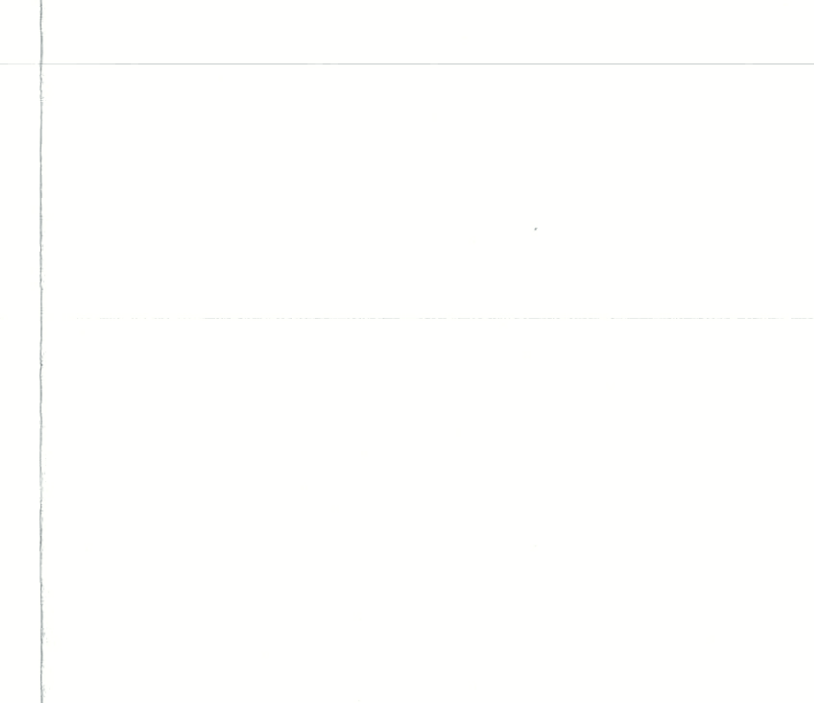

Planzeichenerklärung nach PlanZV 90

|                                                           |   |
|-----------------------------------------------------------|---|
| Art der baulichen Nutzung (§ 9[1] BauGB, §§ 1–11 BauNVO)  |   |
| WA                                                        | Allgemeines Wohngebiet (§ 4 BauNVO)   |
| Maß der baulichen Nutzung (§ 9[1] BauGB, §§ 16–21 BauNVO) |   |
| 0,25                                                      | Grundflächenzahl (GRZ – § 19 BauNVO)   |
| II                                                        | Anzahl der Vollgeschosse (§ 20 BauNVO)   |
| Bauweise (§ 9[2] BauGB, §§ 22,23 BauNVO)                  |   |
| ED                                                        | offene Bauweise (§ 22[2] BauNVO)<br>ED nur Einzel- und Doppelhäuser zulässig                                                                                   |
|                                                           | Baugrenze (§ 23[3] BauNVO)   |
|                                                           | überbaubare Grundstücksfläche (§ 23 BauNVO)   |
| Verkehrsflächen (§ 9[1]1 BauGB)                           |   |
|                                                           | Straßenbegrenzungslinie   |
|                                                           | Öffentliche Straßenverkehrsfläche   |
|                                                           | Private Verkehrsfläche besonderer Zweckbestimmung, mit Geh-, Fahr- und Leitungsrechten zugunsten der Allgemeinheit zu belastende Fläche (§ 9[1]21 u.[6] BauGB) |
| sonstige Planzeichen                                      |   |
|                                                           | Abgrenzung unterschiedlicher Nutzung von Baugebieten oder eines unterschiedlichen Maßes der Nutzung innerhalb von Baugebieten                                  |
| z.B. BE 42,1                                              | Bezugsebene in m über DHNN 92 – hier maßgebende Geländeoberfläche für OK/Rohfußboden Erdgeschoss                                                               |
| z.B. SD 35°–45°                                           | Dachform<br>min. Dachneigung – max. Dachneigung   |
|                                                           | Grenze des räumlichen Geltungsbereiches des Bebauungsplanes (§ 9[7] BauGB)                                                                                     |
| Darstellung ohne Normcharakter                            |   |
|                                                           | vorhandene Flurstücksgrenzen   |
|                                                           | Bestand an Gebäuden   |
|                                                           | Planzeichen nach amtlichem Lageplan   |

Die verwendete Planunterlage enthält den Inhalt des Liegenschaftskatasters und weist die planungsrelevanten baulichen Anlagen sowie Straßen, Wege und Plätze vollständig nach. Sie ist hinsichtlich der planungsrelevanten Bestandteile geometrisch einwandfrei. Die Übertragbarkeit der neu zu bildenden Grenzen in die Örtlichkeit ist einwandfrei möglich.

Birkenwerder, 11.05.2015



2. PLANUNGSRECHTLICHE FESTSETZUNGEN (§ 9 BauGB, BauNVO)  
2.1 Art der baulichen Nutzung (§ 9[1] BauGB, §§ 1–15 BauNVO)  
Allgemeines Wohngebiet (§ 4 BauNVO) – WA –  
– Auf der Grundlage des §1(5) BauNVO sind abweichend von §4(1) BauNVO ausnahmsweise die der Versorgung des Gebietes dienenden Läden, Schank- und Speisewirtschaften zulässig.  
– Auf der Grundlage des §1(5)u.(6) BauNVO sind abweichend von §4(3) BauNVO Betriebe des Beherbergungswesens, Gartenbaubetriebe und Tankstellen nicht zulässig.  
2.2 Maß der baulichen Nutzung (§ 9[1] BauGB, §§ 16–21 BauNVO)  
Zahl der Vollgeschosse (§ 20 BauNVO) und Höhe baulicher Anlagen (§ 18 BauNVO)  
– Auf der Grundlage des §16(2)u.(4) BauNVO wird die Höhe baulicher Anlagen durch zeichnerische Festsetzung der Vollgeschosshöhe nach §20(1) BauNVO als Höchstmaß bestimmt.  
– Der Erdgeschossfußboden (OK Rohfußboden) der Gebäude wird mit max. 0,80 m über der maßgebenden Geländeoberfläche festgesetzt.  
– Auf der Grundlage des §18(1) BauNVO i.V.m. §9(2) BauGB wird die maßgebende Geländeoberfläche als Bezugsebene (BE) in m ü. DHNN 92 zeichnerisch bestimmt.  
Grundflächenzahl (§ 19 BauNVO) – GRZ –  
Die GRZ ist in der jeweiligen Nutzungsschablone festgesetzt.  
2.3 Bauweise und überbaubare Grundstücksfläche (§ 9[1] BauGB, § 22[2] BauNVO)  
Bauweise (§ 22 BauNVO)  
– Auf der Grundlage des §22(2) BauNVO ist eine Form der offenen Bauweise durch konkreten Eintrag in die Nutzungsschablone in den Gebieten zugelassen.  
Überbaubare Grundstücksfläche (§ 23 BauNVO)  
– Auf der Grundlage des §23(1)u.(5) BauNVO sind bauliche Anlagen nur innerhalb der überbaubaren Grundstücksflächen zulässig. Das gilt auch für Nebenanlagen gem. § 14 BauNVO.  
– Anlagen für die technische Versorgung des Gebietes sind ausnahmsweise auch außerhalb der überbaubaren Grundstücksflächen zulässig.  
Stellung baulicher Anlagen  
– Die Lage der straßenseitigen Gebäudeaußenwand ist parallel zur Straßenbegrenzung unter Beachtung der zeichnerischen Festsetzungen von Baugrenzen vorzusehen.  
– Untergeordnete Nebenanlagen und Einrichtungen gem. § 14 BauNVO sowie bauliche Anlagen gem. §23(5)Satz2 BauNVO sind von der Festsetzung "Stellung baulicher Anlagen" nicht betroffen.  
2.4 Größe von Baugrundstücken (§ 9[1]3 BauGB)  
Die Grundstücksgröße ist als Mindestmaß festgesetzt:  
– Errichtung eines Einzelhauses mindestens 580qm.  
– Errichtung einer Doppelhaushälfte mindestens 370qm.  
2.5 Flächen für Stellplätze und Garagen (§ 9[1]4 BauGB)  
Garagen und überdachte Stellplätze gem. §12(2)BauNVO sind auf der Grundlage von §12(6)BauNVO nur innerhalb der überbaubaren Grundstücksfläche zulässig.  
Auf der Grundlage des §12(6)BauNVO sind Stellplätze auf eine Tiefe von 15 m, gerechnet von der Straßenbegrenzung, auch außerhalb der überbaubaren Flächen zulässig.

3. FESTSETZUNGEN ZUR GRÜNORDNUNG  
3.1 Anpflanzung von Bäumen, Sträuchern und sonstigen Bepflanzungen (§ 9 [1] 25 a BauGB)  
a) Je angefangene 500 qm Grundstücksfläche ist ein mittel- bis großkroniger Baum gemäß Artenliste 1 (Hochstamm, Mindeststammumfang 14/16) zu pflanzen.  
b) Auf den privaten Grünflächen sind insgesamt 36 mittel- bis großkronige Bäume gemäß Artenliste A1 (Hochstamm, Mindeststammumfang 12/14) zu pflanzen.  
c) An vorhandenen und neu entstehenden Grundstücksgrenzen, ausgenommen Grundstücksgrenzen zur privaten Verkehrsfläche besonderer Zweckbestimmung, ist jeweils in voller Länge eine einreihige Strauch- bzw. Heckenpflanzung gemäß Artenliste 2 als Einfriedung vorzunehmen (Strauchpflanzung bzw. je lfd.m 3 Stück Heckenpflanzung, Mindestpflanzgröße je 100/125).  
d) Innerhalb der privaten Verkehrsfläche besonderer Zweckbestimmung sind min. 15 Bäume gemäß Artenliste 3 (Hochstamm, Mindeststammumfang 18/20) anzupflanzen.  
e) Alle Baum-, Strauch- und Heckenpflanzungen sind dauerhaft zu erhalten und bei Abgang durch gleichartige Nachpflanzungen zu ersetzen.  
3.2 Versiegelung  
Befestigungen der privaten Verkehrsfläche besonderer Zweckbestimmung, Wege, Zufahrten, Stellplätze, Abstell- sowie Plätze für bewegliche Abfallbehälter sind nur in wasser- und luftdurchlässigem Aufbau herzustellen. Wasser- und Luftdurchlässigkeit wesentlich mindernde Befestigungen sind nicht zulässig.  
3.3 Artenlisten  
Artenliste 1 : Sandbirke ; Hainbuche ; Rot-Dorn ; Apfelkorn ; Walnuss ; Apfel ; Vogelschirke ; Pflaume ; Birne ; Traubeneiche ; Stieleiche ; Mehlebeere ; Eberesche  
Artenliste 2, Sträucher: Roter Hartriegel ; Sandbirke ; Gemeine Heckenkirsche ; Bauernjasmmin ; Myrobalan-Pflaume ; Blut-Johannisbeere ; Büschelrose ; Apfelrose ; Holunder ; Brautspiere ; Gemeiner Flieder ; Gemeiner Schneeball  
Artenliste 2, Hecken: Hainbuche ; Weißdorn ; Gemeiner Liguster ; Alpen-Johannisbeere ; Pyramiden-Hainbuche ; Rot-Dorn ; Apfelkorn ; Eberesche ; Winterlinde  
3.4 Beleuchtung  
Für die Straßenbeleuchtung sind arten- und insektenfreundliche Leuchtmittel zu verwenden.

4. BAUORDNUNGSRECHTLICHE FESTSETZUNGEN, ÖRTLICHE BAUVORSCHRIFTEN (§ 9[4] BauGB i.V.m. § 81 BbgBO)  
4.1 Einfriedungen (i.V.m. § 8 BbgBO)  
Einfriedungen sind entlang der Planstraße nur bis zu einer Höhe von 0,80 m zulässig. Mauern sind nicht zulässig.  
4.2 Dachform, Dachneigung (i.V.m. § 8 BbgBO)  
– Satteldach, Dachneigung 35° – 45°  
– Walmdach, Dachneigung max. 30°  
Flachdächer sind nur für Garagen, Carports und Nebenanlagen gem. § 14(1) BauNVO als Ausnahmen zulässig. Die Firstlinien der Hauptgebüdetelle müssen parallel laufen.  
4.3 Anlagen der Außenwerbung (i.V.m. § 9 BbgBO)  
Anlagen der gem. § 9(2) BbgBO zulässigen Außenwerbung (Werbeanlagen) sind nur i.V.m. der Außenwand im Erdgeschossbereich zulässig. Werbeanlagen mit wechselndem Licht, Lauflichtanlagen und Laserwerbung sind auf der Grundlage des § 81 BbgBO unzulässig.

NACHRICHTLICHE ÜBERNAHME  
1. Belange des Bodendenkmalsschutzes  
Sollten bei Erdarbeiten Bodendenkmale, wie Steinsetzungen, Mauerwerk, Erdverfahrungen, Holzfunde oder -bohlen, Tonscherben, Metallsachen, Münzen, Knochen u.ä. entdeckt werden, sind diese unverzüglich dem Brandenburgischen Landesamt für Denkmalpflege und Archäologischem Landesmuseum, Abteilung Bodendenkmalpflege, oder der unteren Denkmalschutzbehörde anzuzeigen. Die entdeckten Bodendenkmale sind für min. fünf Werktage in unverändertem Zustand zu erhalten (§ 19 [3] BbgSchG).


Verfahrensvermerke

|   |                                             |
|---|---------------------------------------------|
| 1. Aufstellungsbeschluss in öffentlicher Sitzung am 25.11.2014 gefasst. Der Aufstellungsbeschluss ist gemäß Hauptsatzung der Gemeinde Seddiner See bekanntgemacht worden. (§ 2[1] BauGB)   | Axel Zinke<br>Bürgermeister<br>Unterschrift |
| 2. Die für Raumordnung und Landesplanung zuständige Behörde ist gemäß Vertrag über die Aufgaben und Trägerschaft sowie die Aufgaben und Verfahren der gemeinsamen Landesplanung zwischen den Ländern Berlin und Brandenburg (Landesplanungsvertrag, Neufassung vom 01.11.2011) i.V.m. §1(4) BauGB mit Schreiben vom 12.01.2015 beteiligt worden.   | Axel Zinke<br>Bürgermeister<br>Unterschrift |
| 3. Die von der Planung betroffenen Träger öffentlicher Belange und Behörden wurden mit Schreiben vom 12.01.2015 über die Planung unterrichtet und zur Abgabe einer Stellungnahme aufgefordert (§ 4[1] BauGB)   | Axel Zinke<br>Bürgermeister<br>Unterschrift |
| 4. Die Gemeindevertreterversammlung hat am 25.11.2014 den Entwurf der 1. Änderung des Bebauungsplanes in der Fassung –Oktober 2014– gebilligt und beschlossen, diesen sowie den dazugehörigen Entwurf der Begründung öffentlich auszulegen. (§ 3[2] BauGB)   | Axel Zinke<br>Bürgermeister<br>Unterschrift |
| 5. Der Entwurf der 1. Änderung des Bebauungsplanes i.d. Fassung –Oktober 2014– bestehend aus Planteil (Teil A) und Textteil (Teil B), und der Entwurf der Begründung haben in der Zeit vom 12.01.2015 bis 13.02.2015 in der Gemeindeverwaltung der Gemeinde Seddiner See öffentlich ausgelegen. Die Durchführung der Auslegung wurde mit dem Hinweis, dass während der Auslegungsfrist von Jedermann Anregungen und Hinweise schriftlich oder zur Niederschrift vorgebracht werden können, gemäß Hauptsatzung der Gemeinde Seddiner See bekannt gemacht (§ 3[2] BauGB)                                                                                                 | Axel Zinke<br>Bürgermeister<br>Unterschrift |
| 6. Prüfung der von Bürgern und von Trägern öffentlicher Belange vorgebrachten Anregungen und Hinweise durch die Gemeindevertreterversammlung am 28.04.2015. Das Ergebnis ist mitgeteilt worden (§§ 3[2], 4 BauGB)   | Axel Zinke<br>Bürgermeister<br>Unterschrift |
| 7. Der Entwurf der 1. Änderung des Bebauungsplanes in der Fassung –März 2015–, bestehend aus Planteil (Teil A) und Textteil (Teil B) wurde von der Gemeindevertreterversammlung am 28.04.2015 als Satzung beschlossen und die dazugehörige Begründung gebilligt (§ 10 BauGB)   | Axel Zinke<br>Bürgermeister<br>Unterschrift |
| 8. Anzeige der 1. Änderung des Bebauungsplanes in der Fassung –März 2015–, bestehend aus Planteil (Teil A) und Textteil (Teil B), bei der höheren Verwaltungsbehörde (§ 10 BauGB)   | Axel Zinke<br>Bürgermeister<br>Unterschrift |
| 9. Der Verfahrensablauf zur Aufstellung der 1. Änderung des Bebauungsplanes entspricht der gesetzlichen Bestimmung. Die von der Gemeindevertreterversammlung anerkannte Begründung ist vom März 2015. Die 1. Änderung des Bebauungsplanes, bestehend aus Planteil (Teil A) und Textteil (Teil B) wird hiermit ausgearbeitet (§ 11 BauGB)   | Axel Zinke<br>Bürgermeister<br>Unterschrift |
| 10. Die Stelle, bei der die 1. Änderung des Bebauungsplanes auf Dauer während der Dienststunden von jedermann eingesehen werden kann und über den Inhalt Auskunft zu erhalten ist, wurde gemäß § 10(3) BauGB am 20.05.2015 im Amtsblatt der Gemeinde Seddiner See ortsüblich bekanntgemacht. In der Bekanntmachung ist auf die Geltendmachung der Verletzung von Verfahrens- und Formvorschriften und von Mängeln der Abwägung sowie auf die Rechtsfolgen (§215[2] BauGB) und weiter auf Fälligkeit und Erlöschen von Schadensersatzansprüchen (§ 44[3] Satz 1 u.2 sowie [4] BauGB) hingewiesen worden. Die Satzungs ist am 20.05.2015 in Kraft getreten. (§ 12 BauGB) | Axel Zinke<br>Bürgermeister<br>Unterschrift |

Präambel

Aufgrund des § 10 Baugesetzbuches (BauGB), vom 23.09.2004 (BGBl. S.2414), zuletzt geändert durch Gesetz vom 20.11.2014 (BGBl. S.1748), sowie nach § 81 der Brandenburgischen Bauordnung (BbgBO), vom 17.09.2008 (GVBl./08, S.226), zul. geänd. durch Art. 2 d. Gesetzes vom 29.11.2010 (GVBl./10,Nr.39), wird nach Beschlussfassung der Gemeindevertreterversammlung der Gemeinde Seddiner See vom 28.04.2015 und mit Genehmigung der höheren Verwaltungsbehörde diese Satzung über die 1. Änderung des Bebauungsplanes "Generationenpark am See", bestehend aus Planteil (Teil A) und Textteil (Teil B) erlassen.

Übersichtsplan 1:5000

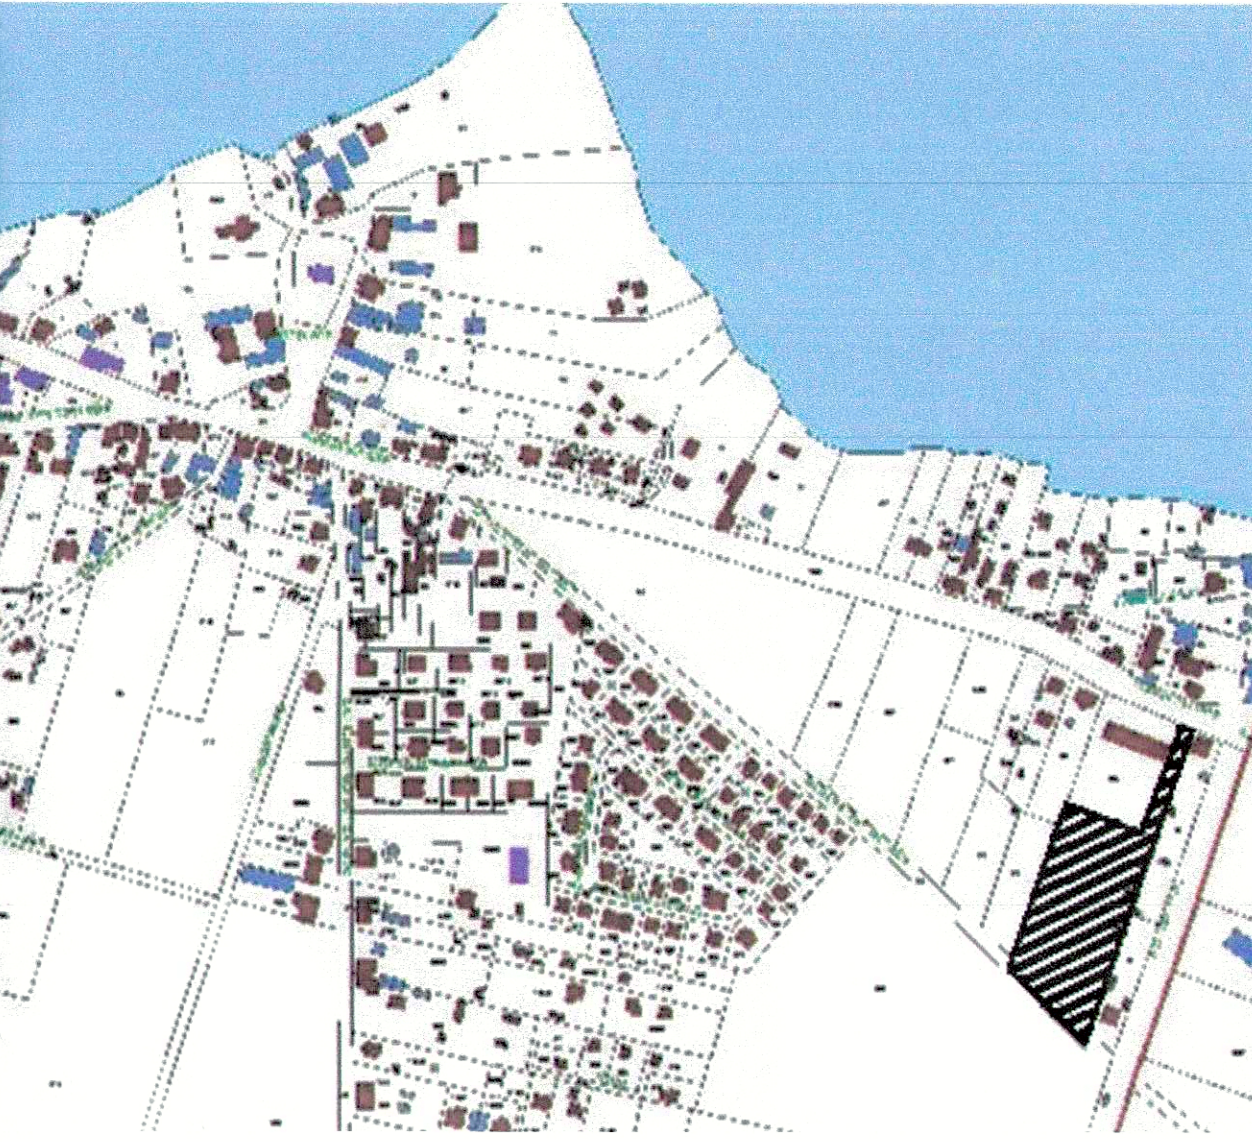

GEMEINDE SEDDINER SEE

Vorhaben: "Generationenpark am See"

Verfahren: 1. Änderung zum Bebauungsplan

- Bestandteile:
- Planteil (Teil A)
  - Planzeichnung
  - Planzeichenerklärung
  - Textteil (Teil B)
  - Rechtsgrundlagen
  - Planungsrechtliche Festsetzungen
  - Grünordnerische Festsetzungen
  - Bauordnungsrechtliche Festsetzungen
  - Nachrichtliche Übernahmen

Beigefügt: Begründung zur 1. Änderung  
Planstand: März 2015

Plangeber: Gemeinde Seddiner See  
vertreten durch:  
Baumit  
Kiefernweg 5  
14554 Seddiner See

Vorhabenträger: Andreas Klein & Detlef Jentsch GbR  
Rothenkruger Weg 77  
12305 Berlin

Auftragnehmer: Dipl.-Ing. walther  
G.-Hauptmann-Str.1  
03099 Kolkwitz