


Übersichtskarte ohne Maßstab

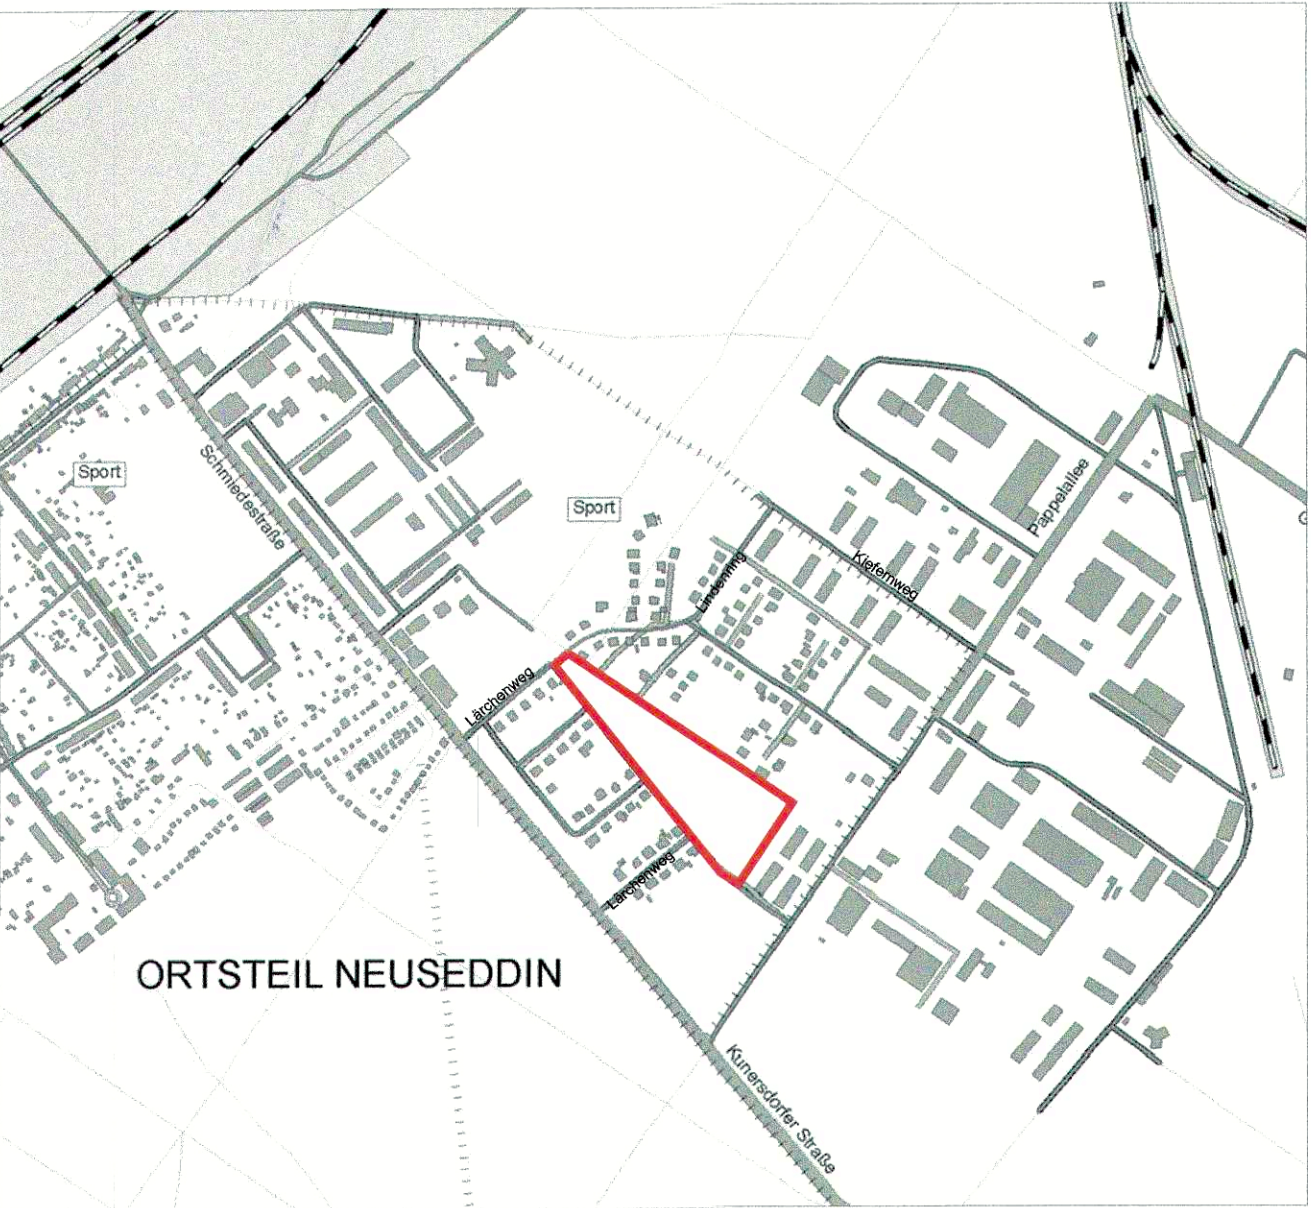

Textliche Festsetzungen

- Im allgemeinen Wohngebiet sind die nach § 4 Abs. 2 BauNVO allgemein zulässigen Läden und Schank- und Speisewirtschaften nicht zulässig.
- Im allgemeinen Wohngebiet sind die in § 4 Abs. 3 BauNVO nach Nr. 4 und Nr. 5 genannten Gartenbaubetriebe und Tankstellen auch ausnahmsweise nicht zulässig.
- Im allgemeinen Wohngebiet darf die Größe der Baugrundstücke 700 m² nicht unterschreiten.
- Im allgemeinen Wohngebiet sind auf den nichtüberbaubaren Grundstücksflächen Garagen und Carports nicht zulässig.
- Im allgemeinen Wohngebiet dürfen Kellergeschosse max. 0,5 m über die Geländeoberkante hinausragen. Geringfügige Überschreitungen sind ausnahmsweise zulässig.
- Im allgemeinen Wohngebiet sind Flachdächer, dh. Dächer mit einer Neigung von weniger als 15 Grad unzulässig.
- Im allgemeinen Wohngebiet ist die Errichtung von Anlagen zur Erzeugung von Heizenergie nicht zulässig.
- Im allgemeinen Wohngebiet ist auf den Flächen A und B die Verwendung von Erdwärmekollektoren und Erdwärmesonden zum Schutz der aktiven Trinkwasserbrunnen nicht zulässig.
- Auf den Baugrundstücken ist eine Befestigung von Stellplätzen, Zufahrten und Wegen wasser- und luftdurchlässig (z. B. Großpflaster mit hohem Fugenanteil, wassergebundene Decke, Schotterrasen, Rasengittersteine) und mit nicht wassergefährdenden, auslaug- und auswaschbaren Materialien herzustellen. Wasser- und Luftdurchlässigkeit mindermende Befestigungen wie Betonunterbau, Fugenverguss oder Asphaltierungen sind unzulässig.
- Je Baugrundstück ist je angefangene 500 m² Grundstücksfläche ein Baum (Stammumfang mindestens 14-16 cm) zu pflanzen. Es sind bei Pflanzungen standortgerechte und einheimische Baumarten zu verwenden. Es wird die Verwendung von Arten der in der Begründung beigefügten Pflanzliste empfohlen.
- Auf den Baugrundstücken sind auf der Fläche zum Anpflanzen von Bäumen, Sträuchern und sonstigen Bepflanzungen mindestens zweireihige Hecken zu pflanzen. Für die Pflanzung ist pro laufender Meter mindestens ein Strauch (Mindestpflanzqualität von zwei Trieben und einer Höhe von 40-60 cm) gemäß der Pflanzliste zu pflanzen.
- Die Einteilung der Straßenverkehrsfläche ist nicht Bestandteil der Festsetzungen.
- Im Geltungsbereich des Bebauungsplans treten alle bisherigen Festsetzungen und baurechtlichen Vorschriften, die verbindliche Regelungen der in § 9 Abs.1 des Baugesetzbuchs bezeichneten Arten enthalten, außer Kraft.

Hinweise

Gemäß § 4 Abs. 1 Bundes-Bodenschutzgesetz (BBodSchG) hat jeder, der auf den Boden einwirkt, sich so zu verhalten hat, dass schädliche Bodenveränderungen und damit mögliche Schadstoffverlagerungen in das Grundwasser nicht hervorgerufen werden können. Des Weiteren ist gemäß § 7 BBodSchG derjenige, der Vorrichtungen auf einem Grundstück durchführt oder durchführen lässt, verpflichtet, Vorsorge gegen das Entstehen schädlicher Boden- und Grundwasserveränderungen zu treffen, die durch ihre Nutzung auf dem Grundstück oder in dessen Einwirkungsbereich hervorgerufen werden können.

Baufeldfreimachungen und der Beginn von Bauarbeiten sind außerhalb der Brutzeiten zwischen 01. Oktober und 28. Februar durchzuführen. Sollten bauvorbereitende Maßnahmen und grundlegende, flächeneingreifende Bauaktivitäten innerhalb dieser Zeit beginnen bzw. sich bis in die Brutzeit hinziehen, wird eine ökologische Baubegleitung empfohlen, um bei spontanen Ansiedlungen von Brutvogelarten rechtzeitig geeignete Maßnahmen zur Vermeidung von artenschutzrechtlichen Verboten ergreifen zu können.

Verfahrensvermerke

Die Gemeindevertretung Seddiner See hat in ihrer Sitzung am 25.09.2012 die Aufstellung des Bebauungsplanes "Lärchenweg" beschlossen. Der Aufstellungsbeschluss ist gem. § 2 Abs. 1 BauGB im Amtsblatt Nr. 04/2013 vom 10.04.2013 öffentlich bekannt gemacht worden.

Seddiner See, den 02.09.2013

Der Bürgermeister

Die verwendete Planunterlage enthält den Inhalt des Liegenschaftskatasters mit Stand vom 01.01.2013 und weist die planungsrelevanten baulichen Anlagen sowie Straßen, Wege und Plätze vollständig nach. Sie ist hinsichtlich der planungsrelevanten Bestandteile geometrisch einwandfrei. Die Übertragbarkeit der neuzubildenden Grenzen in die Örtlichkeit ist einwandfrei möglich.

Datum: 30.08.2013

Öffentlich bestellter Vermessungsingenieur

Siegeldruck

Der Entwurf des Bebauungsplanes vom 04.06.2013 mit Begründung wurde in der Zeit vom 05.07.2013 bis 05.08.2013, montags, mittwochs und donnerstags von 9-12 Uhr und 13-15 Uhr, dienstags von 9-12 und 14-18 Uhr und freitags von 9-12 Uhr in der Gemeindeverwaltung gemäß § 3 Abs. 2 BauGB öffentlich ausgelegt. Die Auslegung wurde im Amtsblatt Nr. 07/2013 vom 26.06.2013 bekannt gemacht.

Seddiner See, den 02.09.2013

Der Bürgermeister

Die Gemeindevertretung hat den Bebauungsplan nach Prüfung der Stellungnahmen der Träger öffentlicher Belange und der Anregungen gem. § 3 Abs. 2 BauGB in ihrer Sitzung am 27.08.2013 als Satzung beschlossen.

Seddiner See, den 02.09.2013

Der Bürgermeister

Die Satzung des Bebauungsplanes wird hiermit ausfertigt.


Seddiner See, den 02.09.2013

Der Bürgermeister

Der Bebauungsplan ist gem. § 10 Abs. 3 BauGB mit der Veröffentlichung im Amtsblatt Nr. 10/2013 vom 04.09.2013 in Kraft getreten. Auf die Frist für die Geltendmachung einer Verletzung von Verfahrens- und Formvorschriften und auf die Vorschriften des § 44 BauGB wurde hingewiesen. Jedermann kann den Bebauungsplan einsehen und über den Inhalt Auskunft erhalten.

Seddiner See, den 05.09.2013

Der Bürgermeister

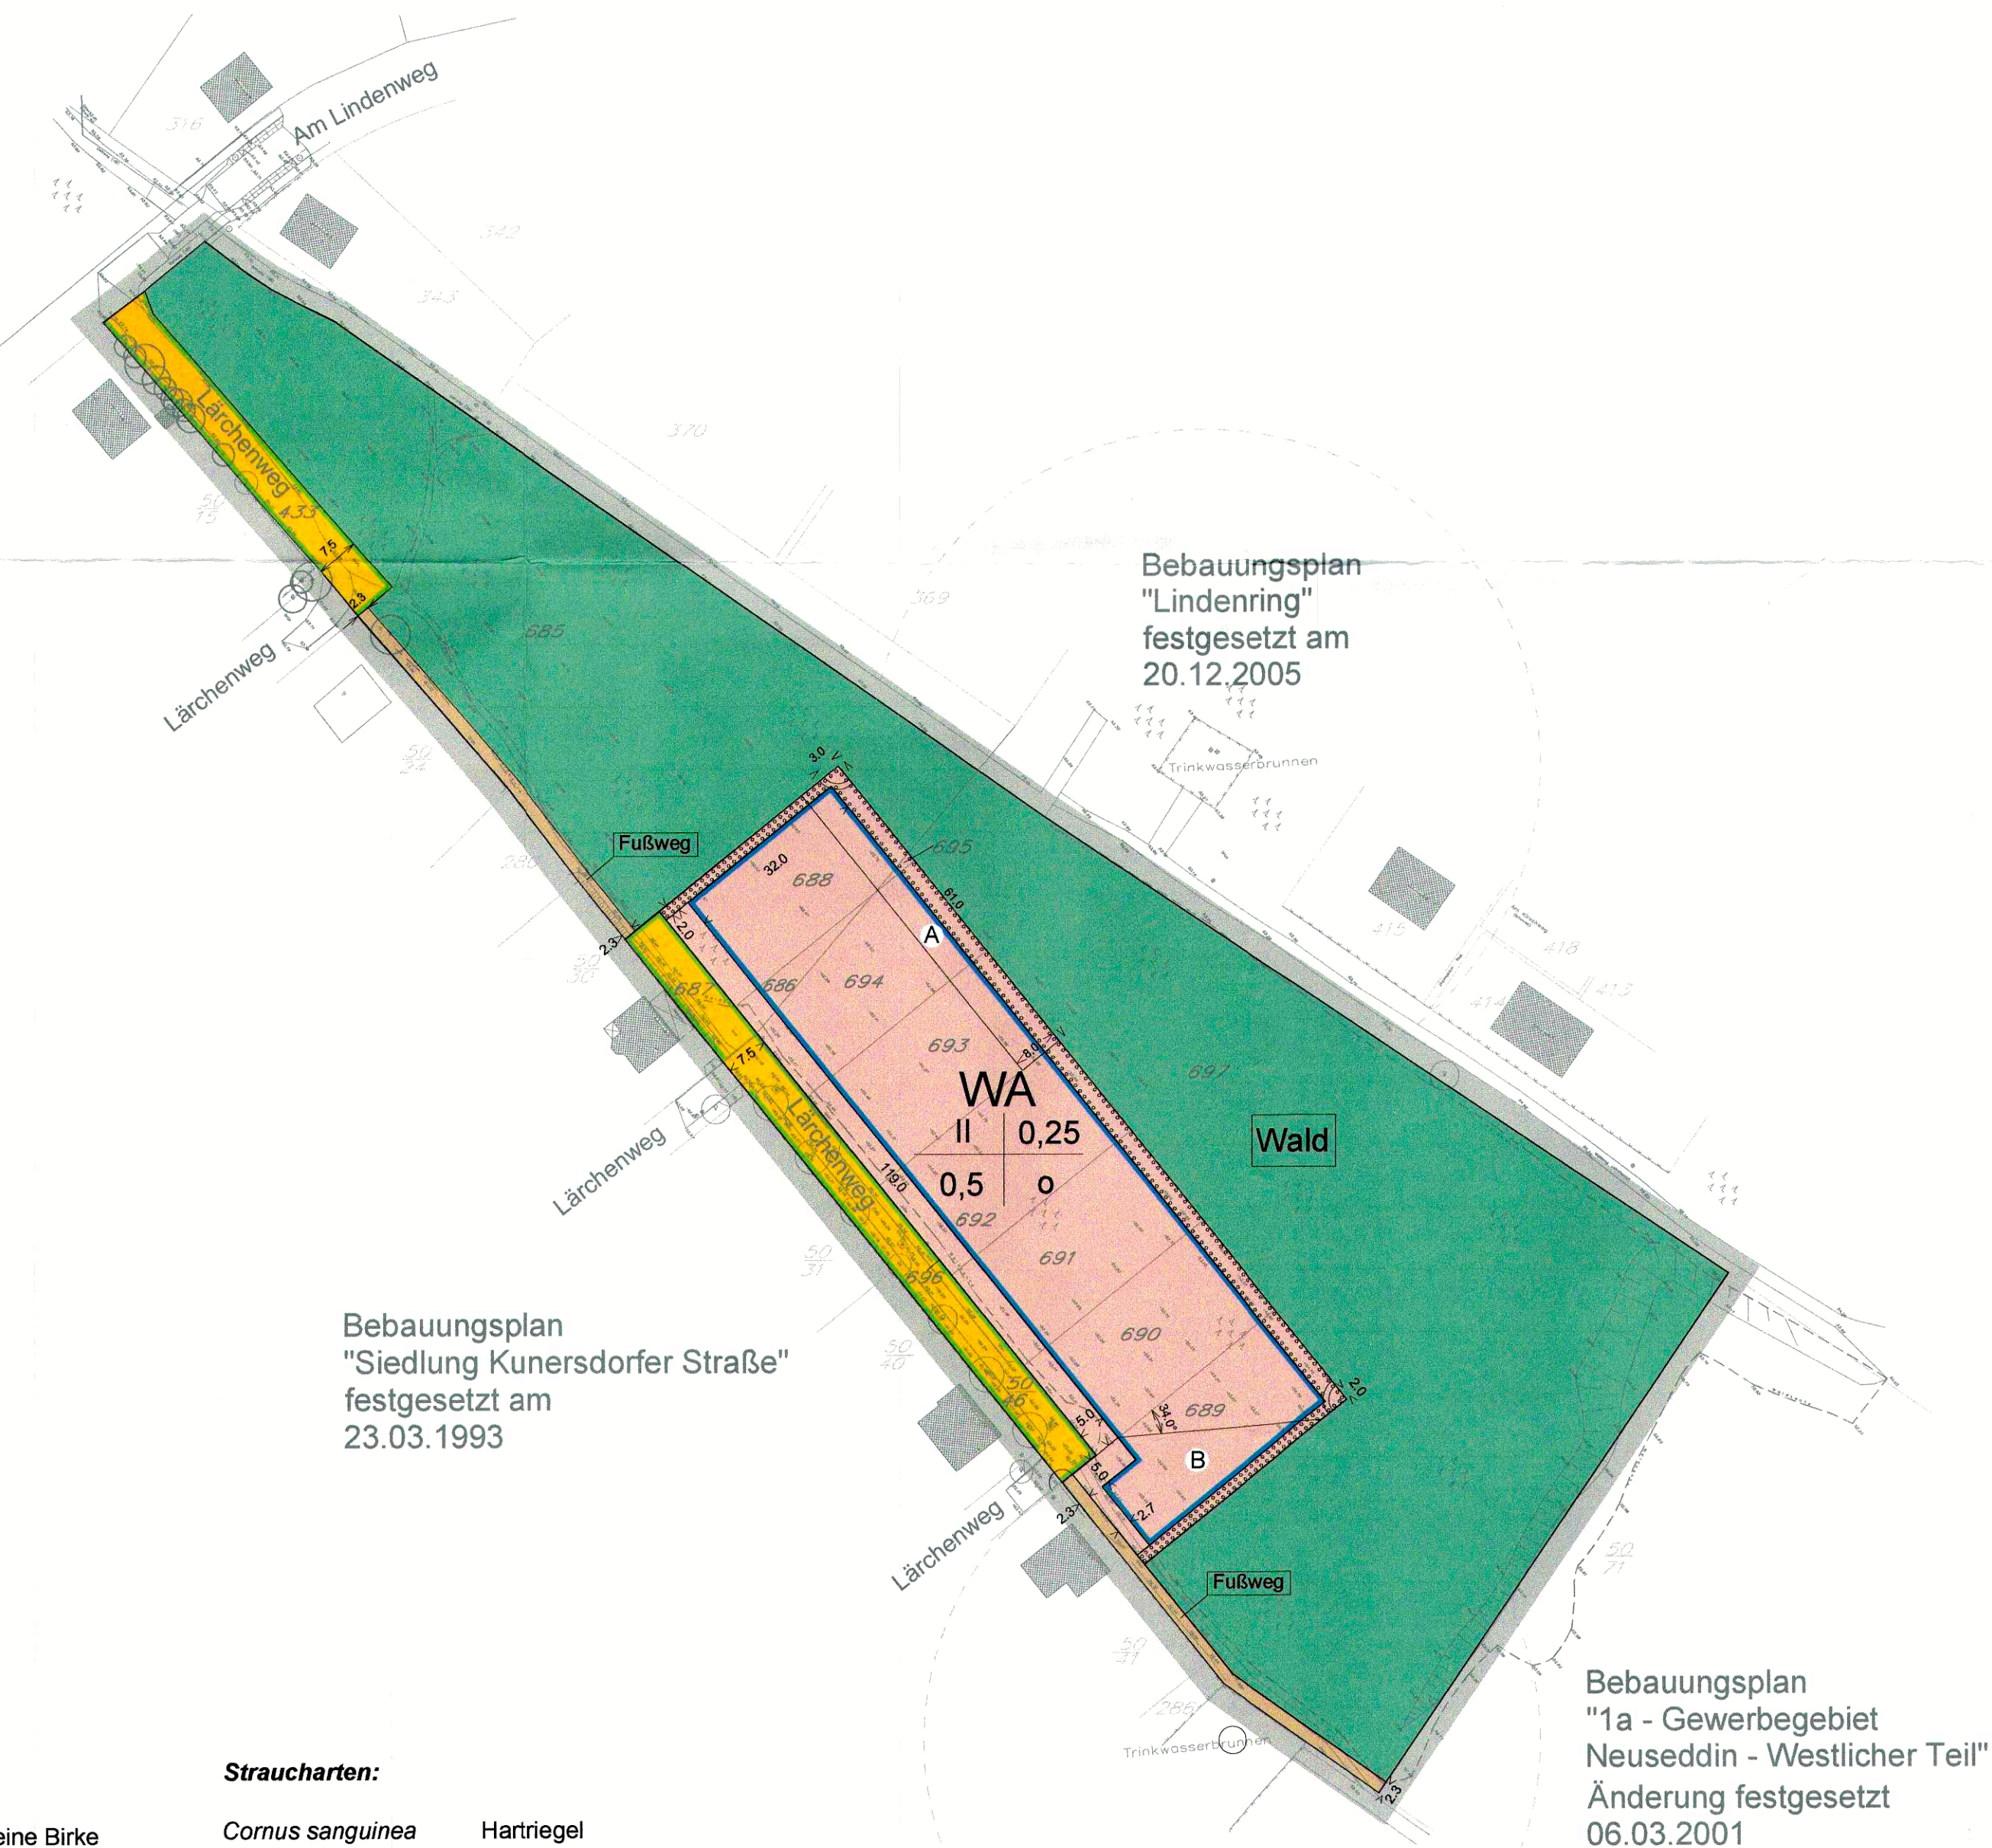

Pflanzliste

Baumarten:

Betula pendula Gemeine Birke
Carpinus betulus Hainbuche
Corylus columa Baumhasel
Prunus avium Vogelkirsche
Prunus padus Traubenkirsche
Quercus petraea Trauben-Eiche
Quercus robur Stiel-Eiche
Sorbus aucuparia Vogelbeere
Tilia cordata Winter-Linde
Tilia platyphyllos Sommer-Linde

Straucharten:

Cornus sanguinea Hartriegel
Crataegus monogyna Zweigriffliger Weißdorn
Lonicera xylosteum Gemeine Heckenkirsche
Prunus spinosa Schlehe
Rhamnus cathartica Kreuzdorn
Rosa canina Hundsrose
Rosa corymbifera Busch-Rose
Rosa rubiginosa Wein-Rose
Rosa tomentosa Filz-Rose
Syringa vulgaris Flieder

Gemeinde Seddiner See
Bebauungsplan "Lärchenweg"

für die Flurstücke 685 tlw., 686, 688 - 695, 697 tlw. und die Straßenflurstücke 50/46 tlw., 433 tlw., 687 und 696 der Flur 2 der Gemarkung Neuseddin im Ortsteil Neuseddin

Zeichenerklärung

Art und Maß der baulichen Nutzung, Bauweise

Allgemeines Wohngebiet (§ 4 BauNVO)
Zahl der Vollgeschosse als Höchstmaß (§ 16 BauNVO)
Grundflächenzahl als Höchstmaß (§ 16 BauNVO)
Geschossflächenzahl als Höchstmaß (§ 16 BauNVO)
offene Bauweise
Baugrenze (§ 23 BauNVO)

Verkehrsflächen

Öffentliche Straßenverkehrsfläche (§ 9 Abs. 1 Nr. 11 BauGB)
Straßenbegrenzungslinie (§ 9 Abs. 1 Nr. 11 BauGB)
öffentliche Verkehrsfläche mit der Zeckbestimmung Fußweg (§ 9 Abs. 1 Nr. 11 BauGB)

Grünflächen

Umgrenzung von Flächen zum Anpflanzen von Bäumen, Sträuchern und sonstigen Bepflanzungen (§ 9 Abs. 1 Nr. 25a BauGB)
Wald (§ 9 Abs.1 Nr. 18b BauGB)

Sonstige Festsetzungen

Geltungsbereichsgrenze (§ 9 Abs. 7 BauGB)

Planunterlage

vorhandene Bebauung
Flurstücksgrenze
Flurstücksnummer, Hausnummer
Bestandsbaum
Laubbaum
Nadelbaum
buschartiges Gehölz
Meßpunkt
Straßenlaterne
Straßenpoller
50-m-Radius um aktive Brunnen

Plangrundlage: Die Vermessung basiert auf dem Höhensystem des Deutschen Haupthöhennetzes 1992 (DHHN 92).
Bezugssystem Lage: ETRS 89
Stand: Oktober 2012

Gemeinde Seddiner See
Bebauungsplan "Lärchenweg"

Auftraggeber: Gemeinde Seddiner See
Kiefernweg 5
14554 Seddiner See

Auftragnehmer: Jahn, Mack & Partner
Alt-Moabit 73
10555 Berlin

Maßstab 1:1000