


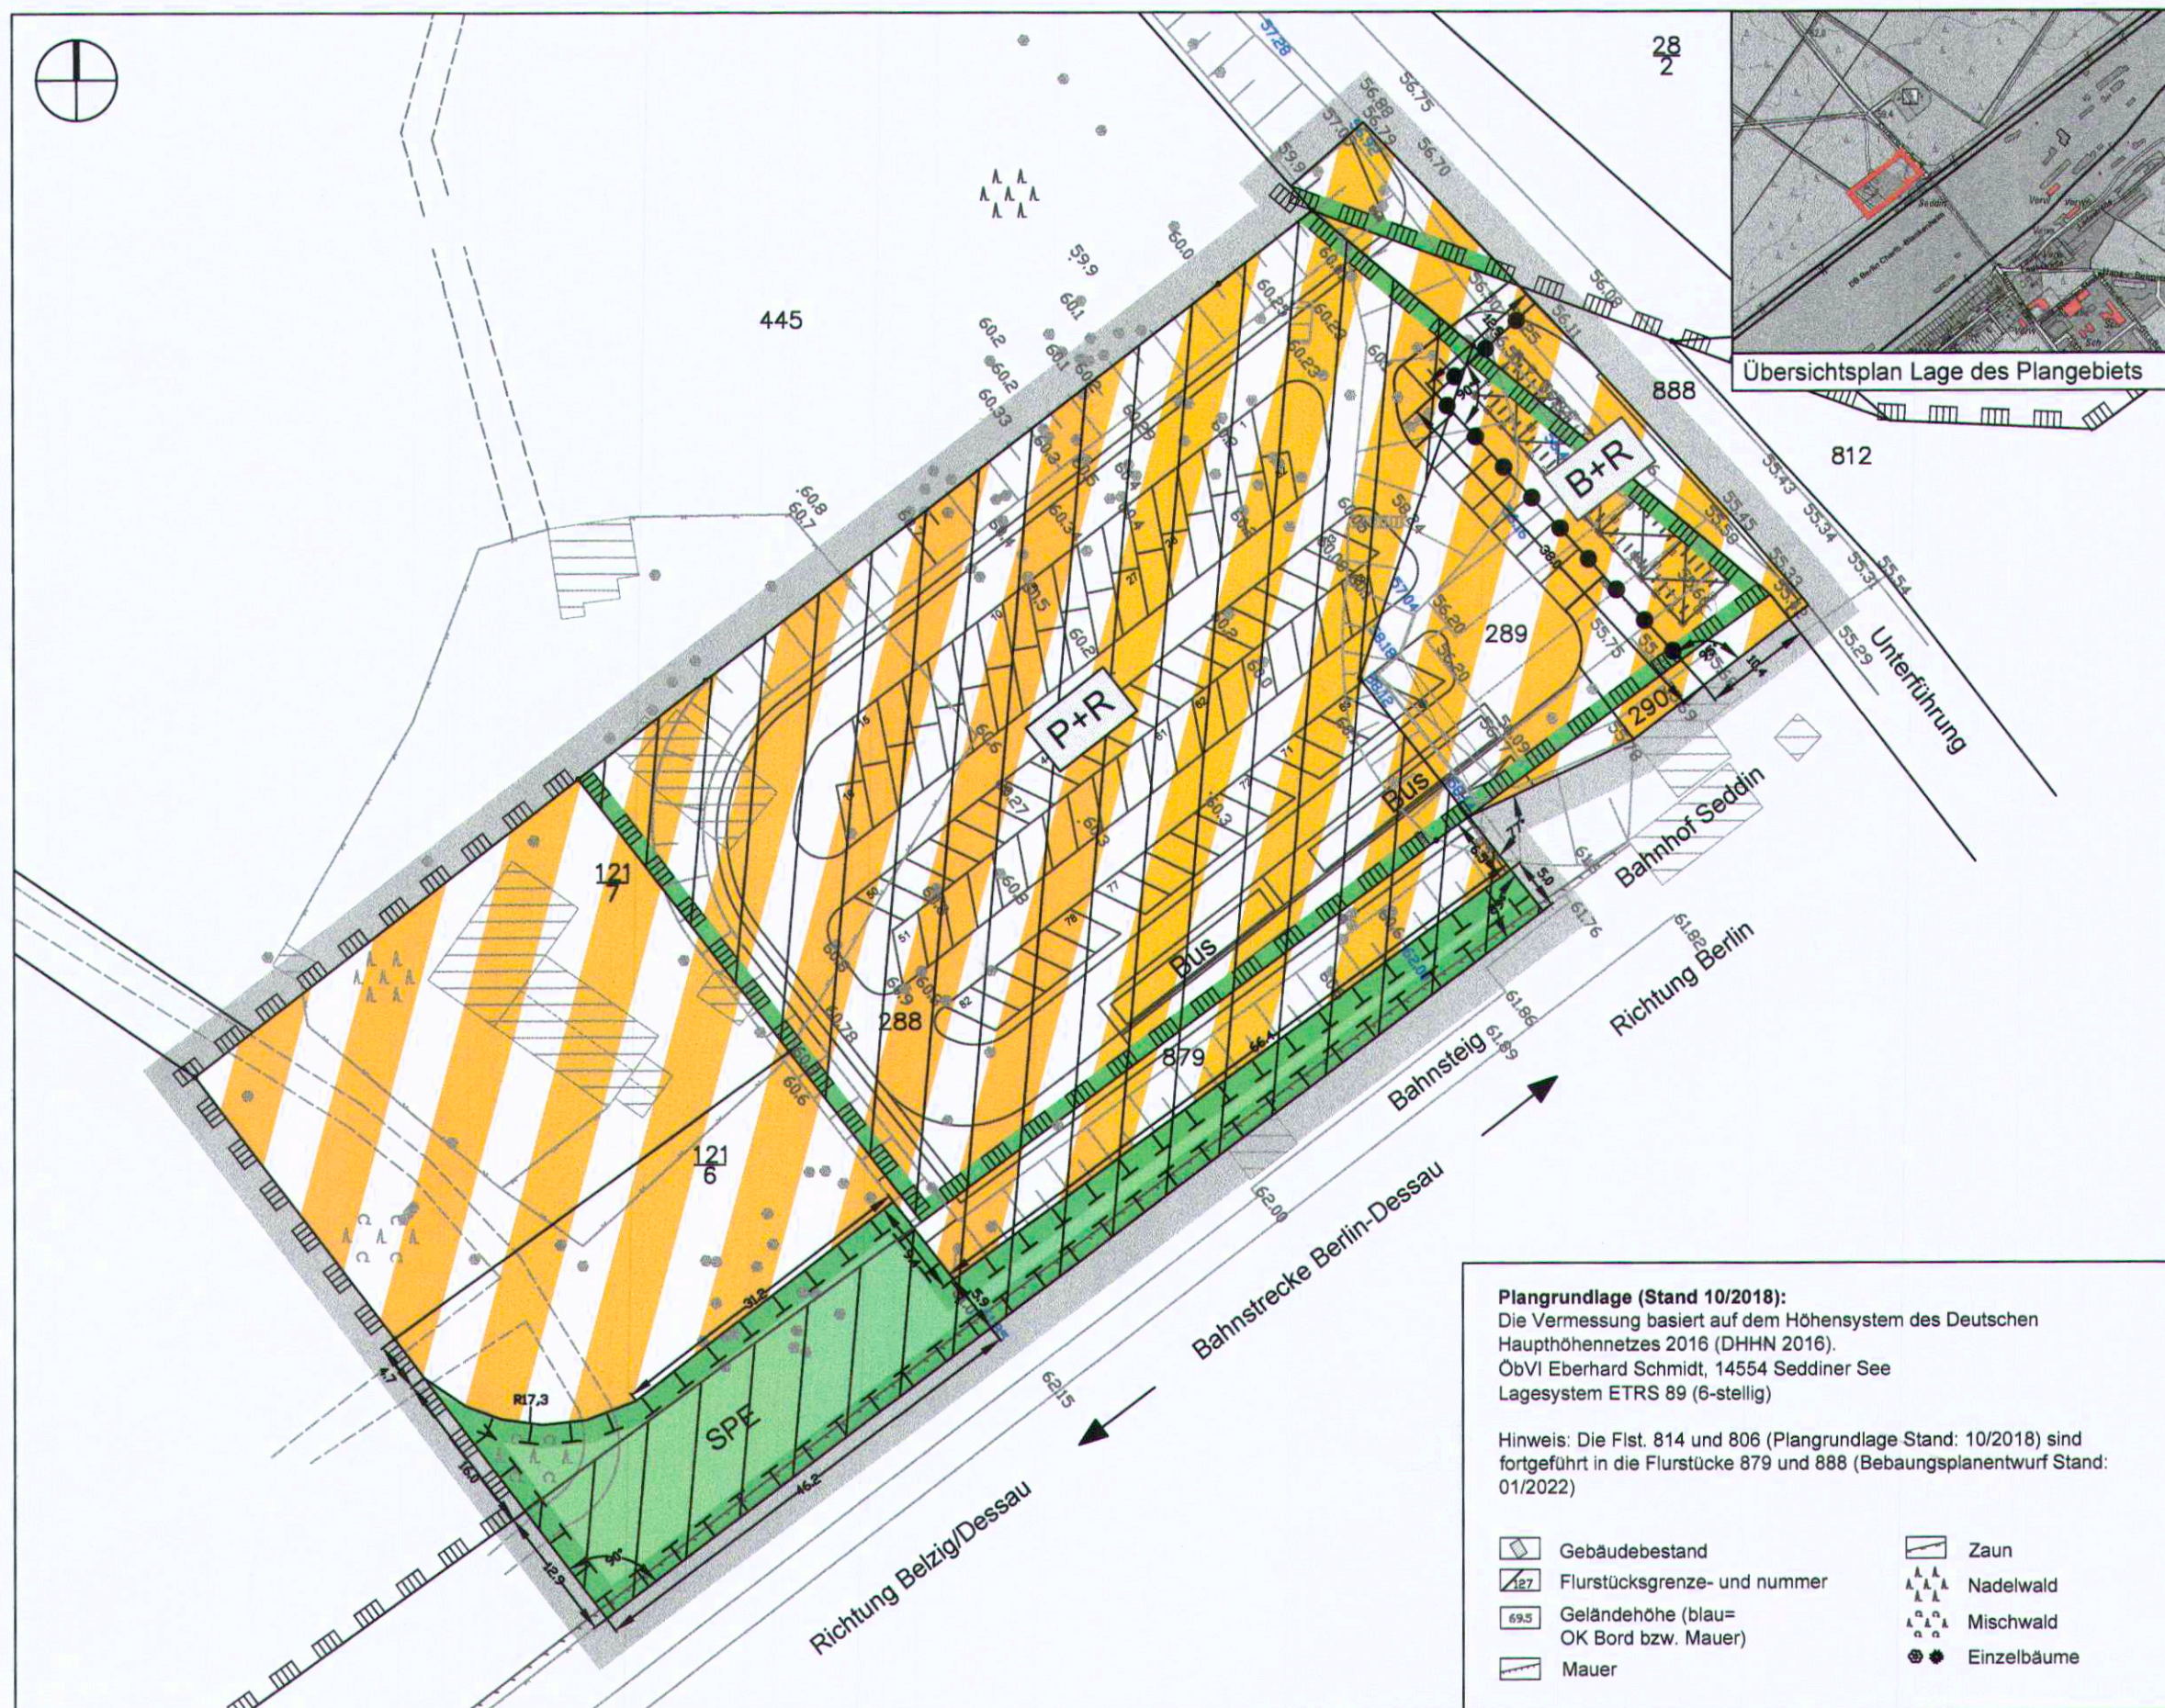

VERFAHRENSVERMERKE

- Die verwendete Planunterlage enthält den Inhalt des Liegenschaftskatasters und weist die planungsrelevanten baulichen Anlagen sowie Straßen, Wege und Plätze vollständig nach. Sie ist hinsichtlich der planungsrelevanten Bestandteile geometrisch einwandfrei. Die Übertragbarkeit der neuzubildenden Grenzen in die Örtlichkeit ist einwandfrei möglich.
- Der Bebauungsplan in der Fassung vom 23. Juni 2022 bestehend aus der Planzeichnung und den textlichen Festsetzungen, wurde am 28. Juni 2022 in der Sitzung der Gemeindevertretung der Gemeinde Seddiner See gemäß § 10 Abs. 1 BauGB als Satzung beschlossen (Beschluss-Nr. 20/Jun./2022). Die Begründung des Bebauungsplans wurde gebilligt.
- Die Satzung des Bebauungsplanes, bestehend aus der Planzeichnung und den textlichen Festsetzungen, wird hiermit ausgefertigt.
- Der Beschluss des Bebauungsplans sowie die Stelle, bei der der Plan auf Dauer während der Dienststunden von jedermann eingesehen werden kann und über deren Inhalt Auskunft zu erhalten ist, sind am 27. Juli 2022 im Amtsblatt Nr. 8/2022 der Gemeinde Seddiner See öffentlich bekannt gemacht worden. Die Satzung tritt mit der Bekanntmachung in Kraft.



PLANZEICHENERKLÄRUNG

- Verkehrsflächen (§ 9 Abs. 1 Nr. 11 und Abs. 6 BauGB)**
- Öffentliche Verkehrsfläche besonderer Zweckbestimmung hier: P+R, B+R und Bus (§ 9 Abs. 1 Nr. 11 und Abs. 6 BauGB)
- Grünflächen (§ 9 Abs. 1 Nr. 15 BauGB)**
- Öffentliche Grünfläche (§ 9 Abs. 1 Nr. 15 BauGB)
- Planungen, Nutzungsregelungen, Maßnahmen und Flächen für Maßnahmen zum Schutz, zur Pflege und zur Entwicklung von Natur und Landschaft (§ 9 Abs. 1 Nr. 20, 25 und Abs. 6 BauGB)**
- SPE** Umgrenzung von Flächen für Maßnahmen zum Schutz, zur Pflege und zur Entwicklung von Natur und Landschaft (§ 9 Abs. 1 Nr. 20 und Abs. 6 BauGB)
- Sonstige Planzeichen**
- Grenze des räumlichen Geltungsbereichs des Bebauungsplans (§ 9 Abs. 7 BauGB)
- Abgrenzung unterschiedlicher Nutzung (§ 9 Abs. 4 BauNVO i.V.m. § 16 Abs. 5 BauNVO)
- Nachrichtliche Übernahme**
- Landschaftsschutzgebiet Potsdamer Wald- und Havelseengebiet (innerhalb Geltungsbereich)
- Landschaftsschutzgebiet Potsdamer Wald- und Havelseengebiet (außerhalb Geltungsbereich)
- Planfestgestellte Bahnflächen (innerhalb Geltungsbereich)
- Darstellung ohne Normcharakter**
- Planungskonzeption (Stationova GmbH, Entwurf November 2021)

TEXTLICHE FESTSETZUNGEN

Textliche Festsetzung Nr. 1

Innerhalb der als Verkehrsfläche besonderer Zweckbestimmung bezeichneten Fläche sind Pkw-Stellplätze, Stellplatzflächen und -anlagen für Fahrräder, Stellplatzflächen für Motorräder, Fahrgassen, Bushaltestellen, Fahrgastunterstände, Beschilderungen, Beleuchtung sowie notwendige konstruktive Elemente des Straßenbaus zulässig.

Die Verkehrsfläche dient auch den Bussen des ÖPNV als Wendeanlage.

(Rechtsgrundlage: § 9 Abs. 1 Nr. 11 und Abs. 6 BauGB)

Textliche Festsetzung Nr. 2

Innerhalb der mit SPE bezeichneten Flächen sind auf maximal 500 qm Gehölze zu erhalten oder Strauchgruppen zu pflanzen. Für Strauchgruppen ist pro 1,5 qm ein Strauch gemäß der Pflanzliste (Mindestpflanzqualität 2x verpflanzt, ohne Ballen, 60-80 cm) zu verwenden.

Die verbleibenden Flächen sind als extensive Wiese anzulegen und mit einer standortgerechten, kräuterreichen Saatgutmischung zu begrünen.

Der innerhalb der Fläche bestehende Gehölzbestand ist bei der Berechnung der Flächengröße der Strauchpflanzungen anzurechnen.

(Rechtsgrundlage: § 9 Abs. 1 Nr. 15 BauGB i.V.m. § 9 Abs. 1 Nr. 20 BauGB)

Textliche Festsetzung Nr. 3

Innerhalb der Verkehrsfläche besonderer Zweckbestimmung sind mindestens 2.101 qm dauerhaft zu begrünen. Der Anteil an Strauchpflanzungen auf den umgebenden Böschungen soll mindestens 700 qm betragen. Es ist pro 1,5 qm ein Strauch (Mindestpflanzqualität 2x verpflanzt, ohne Ballen, 60-80 cm) zu verwenden. Es sind Gehölzarten gemäß der Pflanzliste zu verwenden.

Die verbleibenden Flächen sind als extensive Wiese anzulegen und mit einer standortgerechten, kräuterreichen Saatgutmischung zu begrünen.

Hinweis: Dies gilt nicht für die temporäre Böschung zwischen dem geplanten Bauabschnitt 1 und 2, da sie zum Zeitpunkt der Herstellung des 2. Bauabschnittes zurückgebaut wird.

(Rechtsgrundlage: § 9 Abs. 1 Nr. 25a BauGB)

Textliche Festsetzung Nr. 4

Innerhalb der Verkehrsfläche besonderer Zweckbestimmung sind zur Gliederung der Stellplätze mindestens 28 Laubbäume (Mindestpflanzqualität Hochstamm, Stammumfang 10-12 cm) zu pflanzen. Die Bäume sind in ausreichend große Pflanzscheiben (tatsächlicher Wurzelraum mindestens 9 qm) zu pflanzen.

Es sind Arten gemäß der Pflanzliste zu verwenden.

(Rechtsgrundlage: § 9 Abs. 1 Nr. 25a BauGB)

Textliche Festsetzung Nr. 5

Stellplatzflächen sind nur in wasser- und luftdurchlässigem Aufbau herzustellen. Wasser- und Luftdurchlässigkeit wesentlich mindernde Befestigungen wie Betonunterbau, Fugenvergruss oder Asphaltierungen sind unzulässig.

Dies gilt nicht für Behindertenstellplätze.

(Rechtsgrundlage: § 9 Abs. 1 Nr. 20 BauGB)

HINWEISE

Umgang mit Bodendenkmalen

Sofern bei Erdarbeiten Hinweise auf Bodendenkmale z.B. in Form von Steinsetzungen, Mauerwerk, Erdverfärbungen, Holzpfähle oder -bohlen, Scherben, Knochen, Stein- oder Metallgegenstände entdeckt werden, sind Funde der Unteren Denkmalschutzbehörde und dem Brandenburgischen Landesamt für Denkmalpflege und Archäologischen Landesmuseum unverzüglich anzuzeigen. Der Fund und die Fundstelle sind mindestens bis zum Ablauf einer Woche nach der Anzeige in unverändertem Zustand zu erhalten und in geeigneter Weise vor Gefahren für die Erhaltung des Fundes zu schützen. Funde sind dem Brandenburgischen Landesamt für Denkmalpflege und Archäologischen Landesmuseum zu übergeben.

Waldumwandlung

Innerhalb des Geltungsbereichs des Bebauungsplans „Parken und Umsteigen am Bahnhof Seddin“ ist Wald gem. § 2 LWaldG (Landeswaldgesetz) betroffen, weswegen eine Waldumwandlung erforderlich wird. Der Gesamtverlust beträgt 2.439 qm, davon 998 qm im geplanten Bauabschnitt 1. Die waldrechtlichen Kompensationsanforderungen für den 1. Bauabschnitt sollen abschließend im Bebauungsplan geregelt werden.

Externe Kompensationsflächen

- Auf dem gemeindeeigenen Flurstück 85 der Flur 2 in der Gemarkung Kahnsdorf ist eine 998 qm Fläche mit Waldkiefer, Traubeneiche, Spitzahorn und Hänge-Birke aufzuforsten. Auf der westlichen Seite der Erstaufforstung ist ein gestufter Waldmantel auf 894 qm anzulegen.
- Auf dem gemeindeeigenen Flurstück 85 der Flur 2 in der Gemarkung Kahnsdorf ist eine Streuobstwiese auf 1.674 qm mit mindestens 16 Hochstamm-Obstbäumen auf Grünland (Mindestpflanzqualität 10-12 cm Stammumfang) anzulegen.

- Der Ausgleich für 39 geschützte Einzelbäume kann entweder über Obstgehölze - ein Baum pro 100 m² - innerhalb der Streuobstwiese, Flurstück 85 der Flur 2 in der Gemarkung Kahnsdorf, oder auf anderen Standorten im Gemeindegebiet erbracht werden.

Spezielle Artenschutzmaßnahmen

Vermeidungsmaßnahmen

- Bauzeitenregelung - Baufeldfreimachungen, Gehölzbeseitigungen, Baumfällungen, Rodungen, Abbrucharbeiten sind außerhalb der Vegetationsperiode / Fortpflanzungszeiten der Vögel, sprich in der Zeit vom 01. Oktober bis 28. Februar, durchzuführen.
- Vor den Baumfällungen / Baufeldfreimachungen sind Höhlenbäume nochmals zu kontrollieren (evtl. Neubesiedlung durch den Eremit bzw. nicht einsehbare Höhlen in großer Höhe). Die Kontrolle der Baumhöhlen hinsichtlich des Eremiten kann gleichzeitig mit der Prüfung auf Fledermausbesatz (nur im Sommerhalbjahr nötig) erfolgen.
- Vor Beginn von Baumaßnahmen sind die Zauneidechsen aus dem jeweiligen Baugebiet abzufangen und in die öffentliche Grünfläche/SPE-Fläche im Plangebiet zu vergrämen / auszusetzen. Gefangene andere Reptilien (v.a. Blindschleichen) sind mit umzusetzen.

Vorgezogene Ausgleichsmaßnahme

- Vor Beginn der jeweiligen Baumaßnahmen sind artspezifische Ersatzniststätten für verlustig gehende (Baum-)Höhlen in der unmittelbaren Umgebung des Plangebiets im Verhältnis 1:1 für unbesetzte Baumhöhlen und im Verhältnis 1:2 für besetzte Baumhöhlen aufzuhängen.

Wasserrechtliche Erlaubnis

Sofern das Niederschlagswasser gesammelt und über unterirdische Versickerungsanlagen (z.B. Rigolen, Sickerschächte) ins Grundwasser abgeleitet werden soll, ist mit dem Antrag auf Baugenehmigung eine wasserrechtliche Erlaubnis nach § 8 Abs. 1 des Wasserhaushaltsgesetzes bei der Unteren Wasserbehörde des Landkreises Potsdam-Mittelmark zu beantragen.

Pflanzliste

Baumarten:	
Acer platanoides	Spitz-Ahorn
Acer pseudoplatanus	Berg-Ahorn
Betula pendula	Sand-Birke
Carpinus betulus	Hainbuche
Quercus robur	Stiel-Eiche
Quercus robur 'Fastigiata'	Säulen-Eiche
Tilia cordata i.S.	Winter-Linde
Straucharten:	
Acer campestre	Feld-Ahorn
Cornus sanguinea	Roter Hartriegel
Corylus avellana	Hasel
Crataegus monogyna	Zweiggriffliger Weißdorn
Euonymus europaeus	Pfaffenhütchen
Frangula alnus	Faulbaum
Prunus spinosa	Schlehe
Rhamnus cathartica	Kreuzdorn
Rosa canina	Hundsrose
Rosa corymbifera	Busch-Rose
Sambucus nigra	Schwarzer Holunder
Sorbus aucuparia	Vogelbeere

Normen

Die der Planung zugrunde liegenden Vorschriften (Gesetze, Verordnungen, Erlasse und DIN-Normen) können in der Gemeindeverwaltung

Gemeinde Seddiner See
Kiefernweg 5
14554 Seddiner See

eingesehen werden.

Gemeinde Seddiner See



Bebauungsplan "Parken und Umsteigen am Bahnhof Seddin"

Flst. 288, 289, 290, 121/6 sowie 121/7
Teilfläche Flst. 888, Teilfläche Flst. 879
(Gemarkung Neuseddin, Flur 2)

Satzungsfassung
Stand: 23.06.2022
Maßstab: 1:750 auf A2

Auftraggeber:
Gemeinde
Seddiner See
Kiefernweg 5
14554 Seddiner See

Auftragnehmer:
Jahn, Mack & Partner
architektur und stadtplanung mbB
Wilhelm-Kabus-Straße 74
10829 Berlin

