


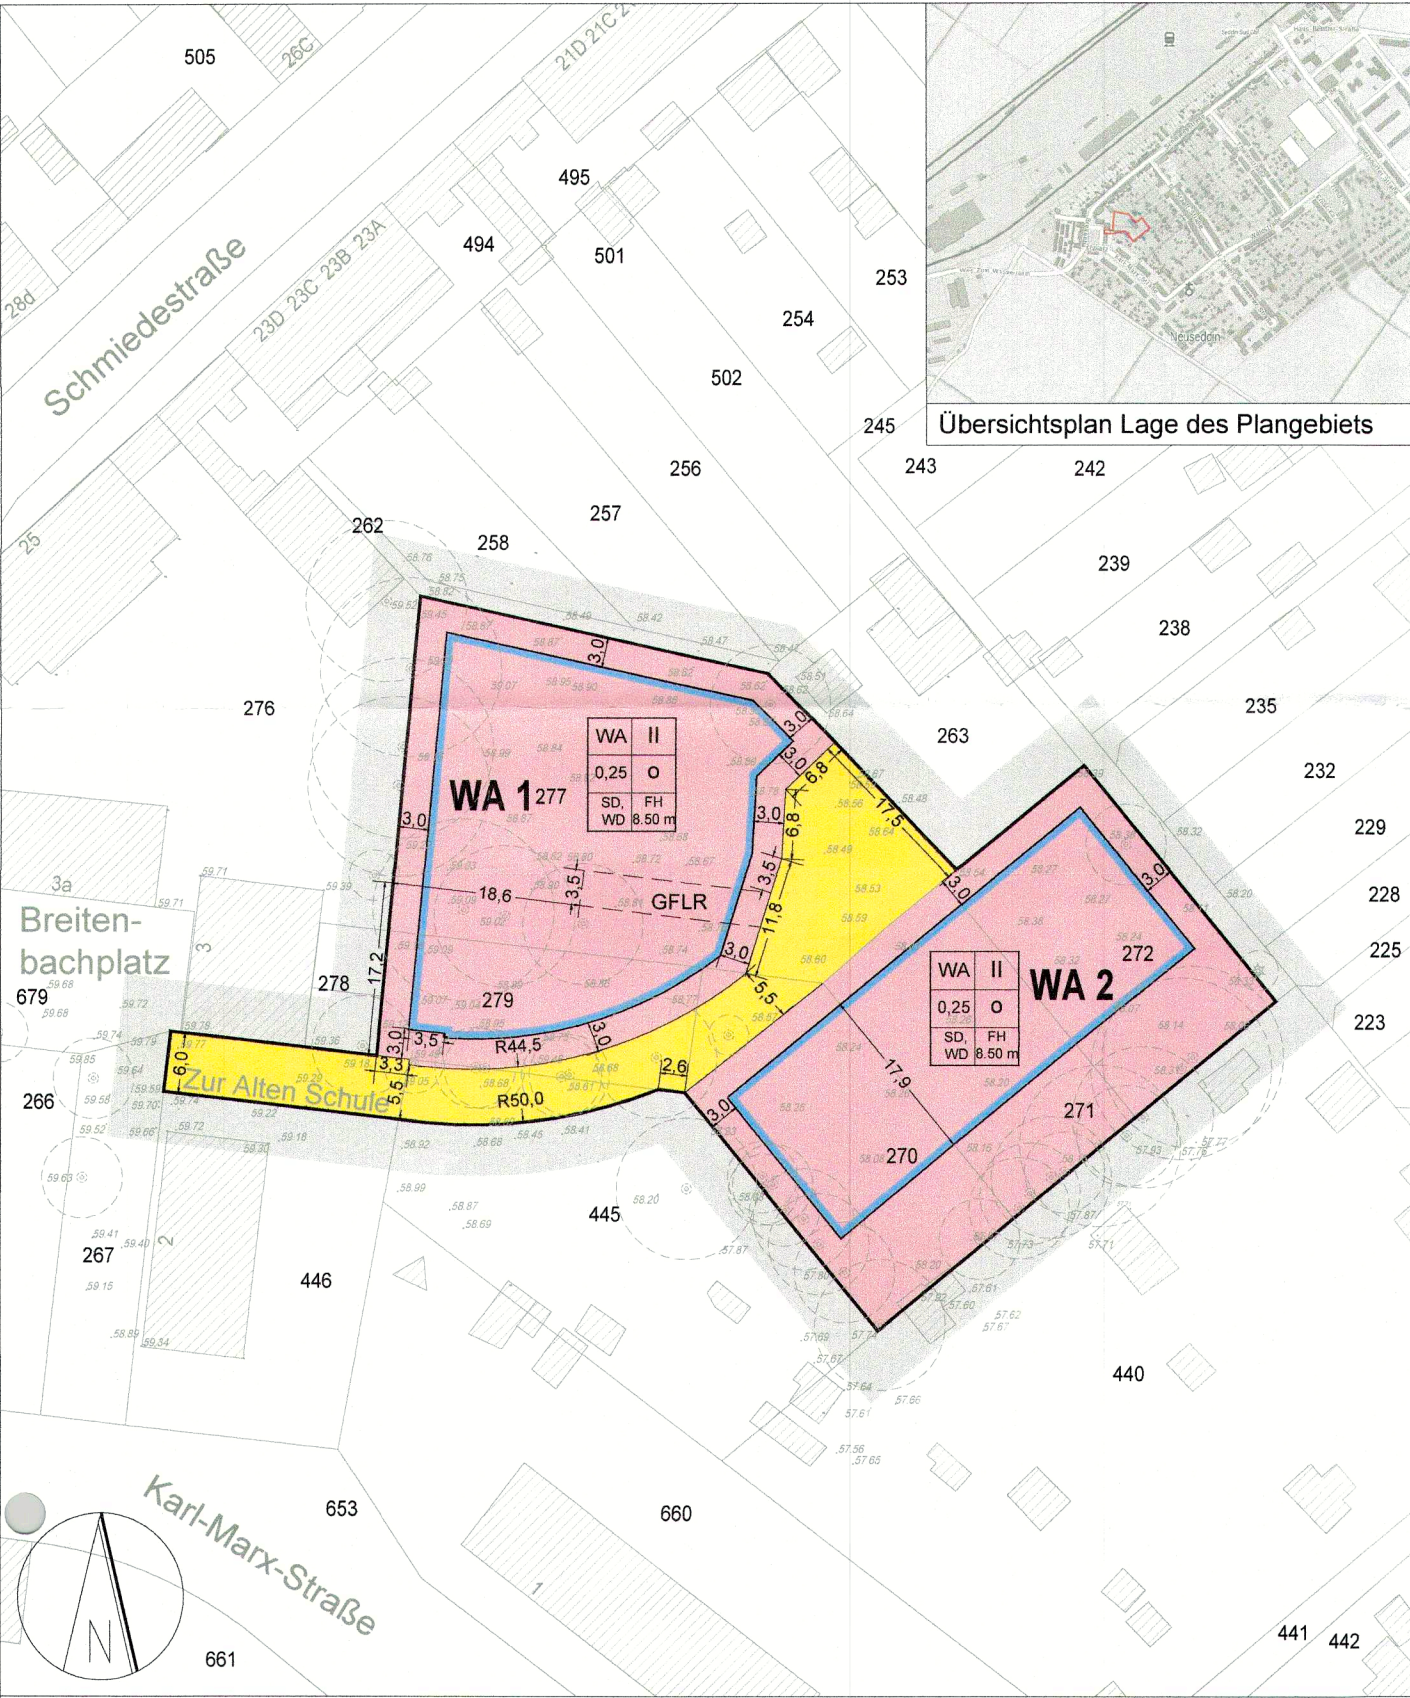

Übersichtsplan Lage des Plangebiets

VERFAHRENSVERMERKE

- 1. Die verwendete Planunterlage enthält den Inhalt des Liegenschaftskatasters und weist die planungsrelevanten baulichen Anlagen sowie Straßen, Wege und Plätze vollständig nach. Sie ist hinsichtlich der planungsrelevanten Bestandteile geometrisch einwandfrei. Die Übertragbarkeit der neuzubildenden Grenzen in die Örtlichkeit ist einwandfrei möglich.
- 2. Der Bebauungsplan in der Fassung vom 10. Mai 2023, bestehend aus der Planzeichnung und den textlichen Festsetzungen, wurde am 11. Juli 2023 in der Sitzung der Gemeindevertretung der Gemeinde Seddiner See gemäß § 10 Abs. 1 BauGB als Satzung beschlossen (Beschluss-Nr. 27. Juli 2023). Die Begründung des Bebauungsplans wurde gebilligt.
- 3. Die Satzung des Bebauungsplanes, bestehend aus der Planzeichnung und den textlichen Festsetzungen, wird hiermit ausgefertigt.
- 4. Der Beschluss des Bebauungsplans sowie die Stelle, bei der der Plan auf Dauer während der Dienststunden von jedermann eingesehen werden kann und über deren Inhalt Auskunft zu erhalten ist, sind am 26. Juli 2023 im Amtsblatt Nr. 7. Juli 2023 der Gemeinde Seddiner See öffentlich bekannt gemacht worden. Die Satzung tritt mit der Bekanntmachung in Kraft.

Seddiner See, den 10. Mai 2023
(ÖbVI)

Seddiner See, den 11. Juli 2023
Bürgermeisterin

Seddiner See, den 13. Juli 2023
Bürgermeisterin

Seddiner See, den 27. Juli 2023
Bürgermeisterin

PLANZEICHENERKLÄRUNG

Art der baulichen Nutzung
(§ 9 Abs. 1 Nr. 1 BauGB i.V.m. §§ 1-11 BauNVO)

Allgemeine Wohngebiete
(§ 4 BauNVO)

Maß der baulichen Nutzung
(§ 9 Abs. 1 Nr. 1 BauGB, i.V.m. §§ 16-21 BauNVO)

- GRZ 0,25 Grundflächenzahl
- II Anzahl der Vollgeschosse
- SD,WD Satteldach, Walmdach
- FH 8,5m Firsthöhe

Bauweise, Baulinien, Baugrenzen
(§ 9 Abs. 1 Nr. 2 BauGB, i.V.m. §§ 22-23 BauNVO)

- O offene Bauweise
- Baugrenze

Verkehrsflächen
(§ 9 Abs. 1 Nr. 11 BauGB)

Private Straßenverkehrsfläche

Sonstige Planzeichen

- Grenze des räumlichen Geltungsbereichs des Bebauungsplans (§ 9 Abs. 7 BauGB)
- Mit Geh-, Fahr- und Leitungsrechten zu belastende Fläche (GFLR) (§ 9 Abs. 1 Nr. 21 BauGB)

Nutzungsschablone

WA II	Art der baulichen Nutzung	Anzahl der Vollgeschosse
0,25 O	Grundflächenzahl	Bauweise
SD, WD 8,50 m	Satteldach, Walmdach	maximal zulässige Firsthöhe

Plangrundlage (Stand: 08/2021)

- Gebäudebestand mit Hausnummer
- Flurstücksgrenze mit Flurstücksnummer
- Einzelbaum
- Geländehöhe in m über NHN (DHHN 2016)

GESETZLICHE GRUNDLAGEN DES BEBAUUNGSPLANS

- Baugesetzbuch in der Fassung der Bekanntmachung vom 3. November 2017 (BGBl. I S. 3634), das zuletzt durch Artikel 2 des Gesetzes vom 4. Januar 2023 (BGBl. 2023 I Nr. 6) geändert worden ist
- Baunutzungsverordnung in der Fassung der Bekanntmachung vom 21. November 2017 (BGBl. I S. 3786), die zuletzt durch Artikel 3 des Gesetzes vom 4. Januar 2023 (BGBl. 2023 I Nr. 6) geändert worden ist
- Bundesnaturschutzgesetz vom 29. Juli 2009 (BGBl. I S. 2542), das zuletzt durch Artikel 3 des Gesetzes vom 8. Dezember (BGBl. I S. 2240) geändert worden ist
- Brandenburgisches Ausführungsgesetz zum Bundesnaturschutzgesetz (Brandenburgisches Naturschutzausführungsgesetz - BbgNatSchAG) vom 21. Januar 2013 (GVBl./13, [Nr. 03], S., berl. GVBl./13 [Nr. 21]), zuletzt geändert durch Artikel 1 des Gesetzes vom 25. September 2020 (GVBl./20, [Nr. 28])
- Brandenburgische Bauordnung (BbgBO) in der Fassung der Bekanntmachung vom 15. November 2018 (GVBl./18, [Nr. 39]), zuletzt geändert durch Artikel 1 des Gesetzes vom 9. Februar 2021 (GVBl./21, [Nr. 5])
- Brandenburgisches Wassergesetz (BbgWG) in der Fassung der Bekanntmachung vom 02. März 2012 (GVBl./12, [Nr. 20]), zuletzt geändert durch Artikel 1 des Gesetzes vom 04. Dezember 2017 (GVBl./17, [Nr.28])
- Planzeichenverordnung vom 18. Dezember 1990 (BGBl. 1991 I S. 58), die zuletzt durch Artikel 3 des Gesetzes vom 14. Juni 2021 (BGBl. I S. 1802) geändert worden ist
- Kommunalverfassung des Landes Brandenburg (BbgKVerf) vom 18. Dezember 2007 (GVBl./07, [Nr. 19], S.286) zuletzt geändert durch Artikel 3 des Gesetzes vom 30. Juni 2022 (GVBl./22, [Nr. 18], S.6)

TEXTLICHE FESTSETZUNGEN

Art der baulichen Nutzung

- 1. WA = Allgemeines Wohngebiet
Allgemein zulässig sind
 - Wohngebäude.Ausnahmsweise können zugelassen werden
 - die der Versorgung des Gebiets dienenden Läden, Schank- und Speisewirtschaften sowie nicht störende Handwerksbetriebe,
 - Anlagen für kirchliche, kulturell, soziale, gesundheitliche und sportliche Zwecke,
 - Betriebe des Beherbergungsgewerbes,
 - sonstige nicht störende Gewerbebetriebe,
 - Anlagen der Verwaltung.Unzulässig und nicht Teil des Bebauungsplans sind
 - Gartenbaubetriebe,
 - Tankstellen.

Höhe baulicher Anlagen

- 2. Die festgesetzten Höhen baulicher Anlagen gelten nicht für technische Aufbauten wie Schornsteine, Lüftungsanlagen und Solaranlagen. Die festgesetzte Firsthöhe kann ausnahmsweise um bis zu 1,0 m überschritten werden.

Überbaubare und nicht überbaubare Grundstücksfläche

- 3. Stellplätze, Garagen und Nebenanlagen i. S. d. § 14 BauNVO sind außerhalb der überbaubaren Grundstücksfläche zulässig.

Mindestgröße von Baugrundstücken

- 4. Im Allgemeinen Wohngebiet müssen die Wohnbaugrundstücke eine Mindestgröße von 500 m² aufweisen.

Verkehrsflächen

- 5. Die Einteilung der Straßenverkehrsflächen ist nicht Gegenstand der Festsetzungen.

Mit Rechten zu belastende Flächen

- 6. Die Fläche mit der Bezeichnung GFLR ist mit einem Geh-, Fahr- und Leistungsrecht zugunsten der Anlieger und mit einem Geh-, Fahr- und Leitungsrecht zugunsten der Ver- und Entsorgungsträger zu belasten.

Grünordnerische Festsetzungen

- 7. Im Allgemeinen Wohngebiet sind Stellplätze, ihre Zufahrten sowie Wege und Terrassen nur in wasser- und luftdurchlässigem Aufbau herzustellen (z.B. Plattenbelag in Splitt, Großpflaster mit hohem Fugenanteil, wassergebundene Decke, Schotterrasen, Rasengittersteine). Auch Wasser- und Luftdurchlässigkeit wesentlich mindernde Befestigungen, wie Betonunterbau, Fugenverguss, Asphaltierungen und Betonierungen, sind unzulässig.
- 8. Die nicht überbauten und nicht gem. § 14 Abs. 1 Satz 1 der Baunutzungsverordnung versiegelten Grundstücksflächen sind zu begrünen oder gärtnerisch anzulegen. Das Anlegen von Schotter-, Splitt-, Kies- und Schieferflächen sowie das Abdichten des Untergrunds mit Folien etc. (sog. Schottergärten) ist unzulässig.
- 9. Im Allgemeinen Wohngebiet ist je vollendete 500 m² Grundstücksfläche, jedoch pro Grundstück mindestens ein Laubbaum mit einem Mindest-Stammumfang von 10-12 cm zu pflanzen, zu erhalten und bei Abgang zu ersetzen. Es ist eine Baumart der Pflanzliste zu verwenden. Alternativ dazu kann ein Hochstamm-Obstbaum starkwüchsiger Sorten (Süßkirsche, Apfel, Birne und Pflaume) gepflanzt werden.

Pflanzliste:

- | | |
|-----------------------------------|------------------------|
| Acer campestre | Feld-Ahorn |
| Acer platanoides 'Globosum' | Kugelahorn |
| Acer pseudoplatanus | Berg-Ahorn |
| Aesculus x carnea 'Briotii' | Scharlach Rosskastanie |
| Betula pendula | Gemeine Birke |
| Carpinus betulus i.S. | Hainbuche |
| Crataegus x lavallei 'Carrierei' | Apfeldorn |
| Fagus sylvatica | Rotbuche |
| Fraxinus excelsior | Gemeine Esche |
| Prunus padus | Traubenkirsche |
| Quercus coccinea 'Fastigiata' | Säulenscharlacheiche |
| Quercus petraea | Trauben-Eiche |
| Quercus robur | Stiel-Eiche |
| Quercus robur 'Fastigiata Koster' | Säuleneiche |
| Sorbus aucuparia | Vogelbeere |
| Sorbus intermedia | Schwedische Mehlbeere |
| Tilia cordata | Winter-Linde |
| Ulmus laevis | Flatter-Ulme |
| Ulmus minor | Feld-Ulme |
| Salix caprea | Sal-Weide |
| Malus sylvestris | Wildapfel |
| Malus i.S. | Zierapfel |
| Pyrus pyrastrer | Wildbirne |
| Prunus avium | Wildkirsche |

Festsetzungen zum Schutz vor Lärm

- 10. Zum Schutz vor Verkehrslärm müssen bei Errichtung, Änderung oder Nutzungsänderung von baulichen Anlagen die Außenbauteile schutzbedürftiger Aufenthaltsräume der Gebäude im Geltungsbereich des Bebauungsplans ein bewertetes Gesamt- Bauschalldämm-Maß (R'w,ges) aufweisen, das nach folgender Gleichung gemäß DIN 4109-1:2018-01 zu ermitteln ist:
R'w,ges = La - KRaumart
mit La = maßgeblicher Außenlärmpegel
mit KRaumart = 30 dB für Aufenthaltsräume in Wohnungen
= 35 dB für Büroräume und Ähnliches

Die Ermittlung des maßgeblichen Außenlärmpegels La erfolgt hierbei entsprechend Abschnitt 4.4.5.3 gemäß DIN 4109-2:2018-01. Dabei sind die Lüftungstechnischen Anforderungen für die Aufenthaltsräume durch den Einsatz von schalldämmten Lüftern in allen Bereichen mit nächtlichen Beurteilungspegeln > 50 dB(A) zu berücksichtigen.

Der Nachweis der Erfüllung der Anforderungen ist im Baugenehmigungsverfahren zu erbringen. Dabei sind im Schallschutznachweis insbesondere die nach DIN 4109-2:2018-01 geforderten Sicherheitsbeiwerte zwingend zu beachten.

Die zugrunde zu legenden maßgeblichen Außenlärmpegel (La) sind aus den ermittelten Beurteilungspegeln der schalltechnischen Untersuchung abzuleiten, die Bestandteil der Satzungsunterlagen ist. Von den Werten kann abgewichen werden, wenn nachgewiesen wird, dass die dem Schallgutachten zugrunde gelegten Ausgangsdaten nicht mehr zutreffend sind.

Örtliche Bauvorschriften

- 11. Im allgemeinen Wohngebiet sind die Dächer von Gebäuden als Sattel- oder Walmdächer mit Dachneigungen von mindestens 30 Grad auszuführen.
- 12. Im Allgemeinen Wohngebiet sind Dacheindeckungen (z.B. Ziegel oder Dachsteine) nur in Rottönen zulässig.

HINWEISE

zu gesetzlichen Artenschutzmaßnahmen

Bauzeitenregelung: Baufeldfreimachungen, Baustelleneinrichtungen, Gehölzbe-seitigungen sowie Abbrucharbeiten sind außerhalb der Fortpflanzungszeit im Zeitraum 01. Oktober bis 28. Februar durchzuführen.

Bei Verlust von Fortpflanzungsstätten geschützter Vogelarten und Fledermäuse in Baumhöhlen sind in doppelter Anzahl Ersatzniststätten für Vögel und in einfacher Anzahl Ersatzniststätten für Fledermäuse in räumlicher Nähe zu schaffen.

zum Baumschutz

Im Geltungsbereich dieses Bebauungsplans ist die aktuelle Gehölzschutzsatzung in der Gemeinde Seddiner See vom 27.09.2016 (öff. bekannt gemacht 26.10.2016) anzuwenden.

zur Versickerungspflicht auf Grundstücken

Niederschlagswasser aus Grundstücken und Dachentwässerungen dürfen nicht in den öffentlichen Verkehrsraum (Straßen, Wege, Plätze, Grünanlagen) bzw. in die Straßenkanalisation abgeleitet werden, sondern sind auf eigenem Grundstück zu versickern. (§ 4 Abs. 8 Gemeindeordnung vom 03.05.2022, öff. bekannt gemacht 25.05.2022).

zu Lärmemissionen

Durch verschiedene Vorgänge auf dem Rangierbahnhof kann es sowohl am Tag als auch während der Nacht zu Geräuschspitzen oder einzelnen heraushörbaren Geräuschen kommen, so z.B. beim Auflaufen von Wagen, im Bereich der Gleisbremsen etc.

zur Stellplatzsatzung

Im Geltungsbereich dieses Bebauungsplans ist die aktuelle Satzung über die Herstellung notwendiger Stellplätze in der Gemeinde Seddiner See (Stellplatzsatzung) vom 23.08.2005 (öff. bekannt gemacht 12.12.2005) anzuwenden.

zum Umgang mit Bodendenkmalen

Sofern bei Erdarbeiten Hinweise auf Bodendenkmale entdeckt werden, sind Funde der Unteren Denkmalschutzbehörde und dem Brandenburgischen Landesamt für Denkmalpflege und Archäologischen Landesmuseum unverzüglich anzuzeigen. Der Fund und die Fundstelle sind mindestens bis zum Ablauf einer Woche nach der Anzeige in unverändertem Zustand zu erhalten und in geeigneter Weise vor Gefahren für die Erhaltung des Fundes zu schützen. Funde sind dem Brandenburgischen Landesamt für Denkmalpflege und Archäologischen Landesmuseum zu übergeben.

Gemeinde Seddiner See



Bebauungsplan
"Wohnbebauung Alte Schule"

Gemarkung Neuseddin: Flur 1, Flst. 270, 271, 272, 277, 279
445 und 446 teilweise

Stand: 10.05.2023
Maßstab Planzeichnung: 1:750 auf A2

Auftraggeber:
Gemeinde
Seddiner See
Kiefernweg 5
14554 Seddiner See

Auftragnehmer:
Jahn, Mack & Partner
architektur und stadtplanung mbB
Wilhelm-Kabus-Straße 74
10829 Berlin

Plangrundlage (Stand: 08/2021):
Öffentlich bestellter Vermessungsingenieur
Dipl.-Ing. Marten Kirchner

JAHN, MACK & PARTNER
architektur und stadtplanung mbB