


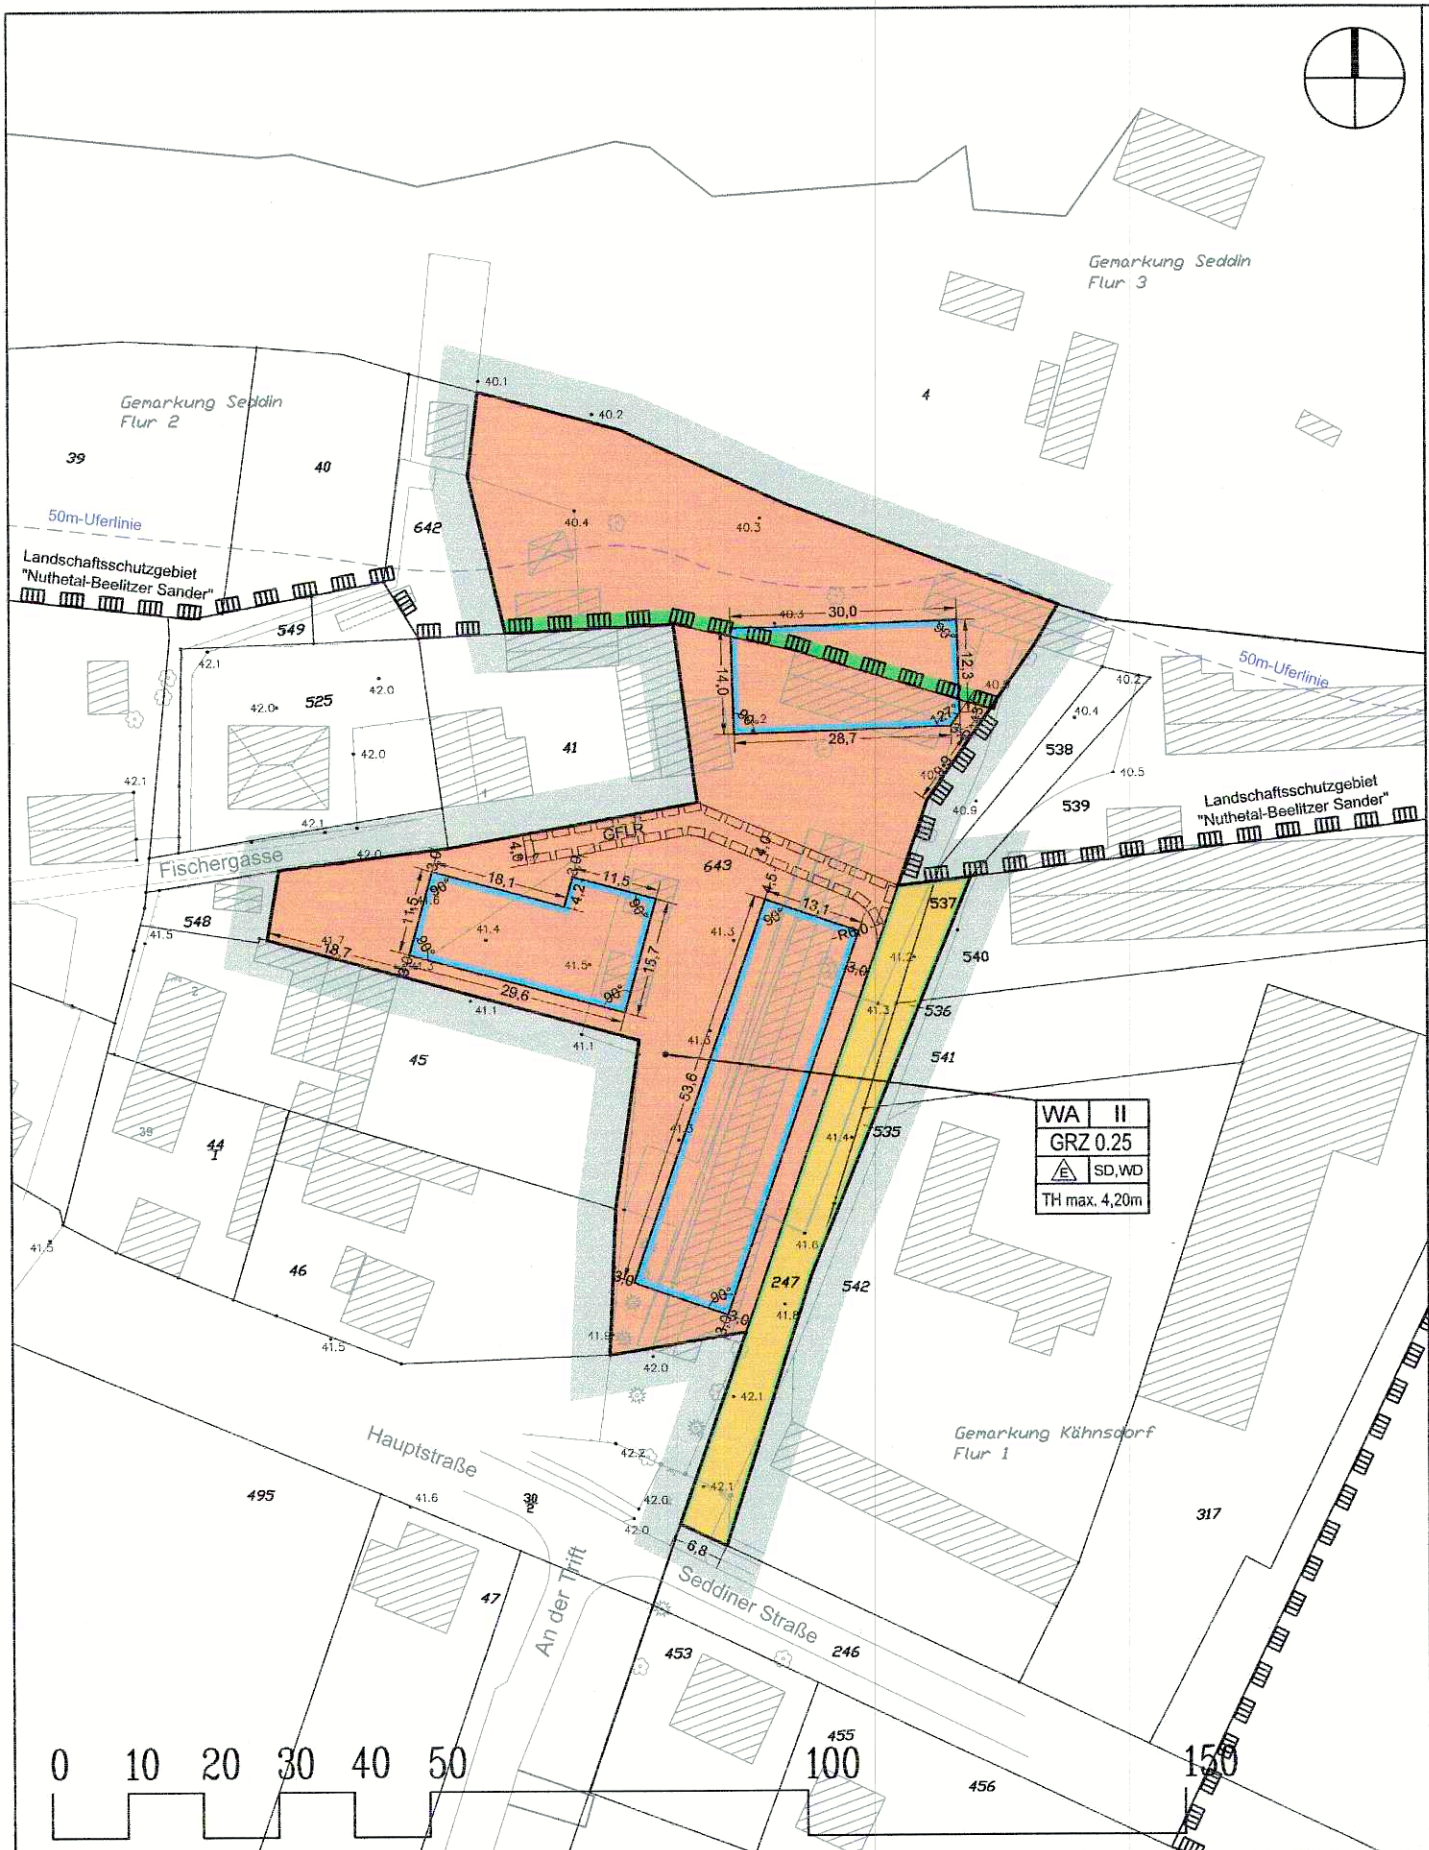

VERFAHRENSVERMERKE

- Die verwendete Planunterlage enthält den Inhalt des Liegenschaftskatasters und weist die planungsrelevanten baulichen Anlagen sowie Straßen, Wege und Plätze vollständig nach. Sie ist hinsichtlich der planungsrelevanten Bestandteile geometrisch einwandfrei. Die Übertragbarkeit der neuzubildenden Grenzen in die Örtlichkeit ist einwandfrei möglich.
- Der Bebauungsplan in der Fassung vom **02.03.2021** bestehend aus der Planzeichnung und den textlichen Festsetzungen, wurde am **29.06.2021** in der Sitzung der Gemeindevertretung der Gemeinde Seddiner See gemäß § 10 Abs. 1 BauGB als Satzung beschlossen (Beschluss-Nr. **03/Jun.2021**). Die Begründung des Bebauungsplans wurde gebilligt.
- Die Satzung des Bebauungsplanes, bestehend aus der Planzeichnung und den textlichen Festsetzungen, wird hiermit ausgefertigt.
- Der Beschluss des Bebauungsplans sowie die Stelle, bei der der Plan auf Dauer während der Dienststunden von jedermann eingesehen werden kann und über deren Inhalt Auskunft zu erhalten ist, sind am **28.03.2021** im Amtsblatt Nr. **07.2021** der Gemeinde Seddiner See öffentlich bekannt gemacht worden. Die Satzung tritt mit der Bekanntmachung in Kraft.

Seddiner See, den **07.04.21**

Seddiner See, den **30.06.2021**

Seddiner See, den **01.07.2021**

Seddiner See, den **29.07.2021**

Eberhard Schmidt
ÖbVI
Bürgermeister

Axel Zinke
Bürgermeister

Axel Zinke
Bürgermeister

Axel Zinke
Bürgermeister

PLANZEICHENERKLÄRUNG

Art der baulichen Nutzung
(§ 9 Abs. 1 Nr. 1 BauGB i.V.m. §§ 1-11 BauNVO)

WA Allgemeine Wohngebiete
(§ 4 BauNVO)

Maß der baulichen Nutzung
(§ 9 Abs. 1 Nr. 1 BauGB, i.V.m. §§ 16-21 BauNVO)

GRZ 0,25 Grundflächenzahl

TH Traufhöhe

II Anzahl der Vollgeschosse

SD, WD Satteldach, Krüppelwalmdach

Bauweise, Baulinien, Baugrenzen
(§ 9 Abs. 1 Nr. 2 BauGB, i.V.m. §§ 22-23 BauNVO)

E nur Einzelhäuser zulässig

B Baugrenze

Verkehrsflächen
(§ 9 Abs. 1 Nr. 11 BauGB)

S Öffentliche Straßenverkehrsfläche

S Straßenbegrenzungslinie

Sonstige Planzeichen

G Grenze des räumlichen Geltungsbereichs des Bebauungsplans
(§ 9 Abs. 7 BauGB)

GFLR Mit Geh-, Fahr- und Leitungsrechten zu belastende Fläche (GFLR)
(§ 9 Abs. 1 Nr. 21 BauGB)

Nachrichtliche Übernahmen

L Landschaftsschutzgebiet "Nuthetal-Beelitzer Sander",
(§9 Abs. 6 BauGB, innerhalb Geltungsbereich)

L Landschaftsschutzgebiet "Nuthetal-Beelitzer Sander",
(§9 Abs. 6 BauGB, außerhalb Geltungsbereich)

U 50 m-Uferlinie (Freihaltung von Gewässern u. Uferzonen gem.
§ 61 BNatSchG, Bauverbote an Gewässern gem. § 48 BbgNatSchG)

Plangrundlage (Stand: 02/2020)

B Gebäudebestand mit Hausnummer

F Flurstücksgrenze mit Flurstücksnummer

E Einzelbaum

H Geländehöhe in m über NHN (DHHN 2016)

Z Zaun

M Mauer

GESETZLICHE GRUNDLAGEN DES BEBAUUNGSPLANS

Baugesetzbuch in der Fassung der Bekanntmachung vom 3. November 2017 (BGBl. I S. 3634), zuletzt geändert durch Artikel 2 des Gesetzes vom 8. August 2020 (BGBl. I S. 1728)

Baunutzungsverordnung in der Fassung der Bekanntmachung vom 21. November 2017 (BGBl. I S. 3786)

Verordnung über die Ausarbeitung der Bauleitpläne und die Darstellung des Planinhalts (Planzeichenverordnung - PlanZV) vom 18. Dezember 1990 (BGBl. 1991 I S. 58), zuletzt geändert durch Artikel 3 des Gesetzes vom 4. Mai 2017 (BGBl. I S. 1057)

Brandenburgische Bauordnung (BbgBO) in der Fassung der Bekanntmachung vom 15. November 2018 (GVBl./18, [Nr. 39]), zuletzt geändert durch Gesetz vom 9. Februar 2021 (GVBl./21, [Nr. 5])

TEXTLICHE FESTSETZUNGEN

Art der baulichen Nutzung

WA = Allgemeines Wohngebiet

Allgemein zulässig sind

- Wohngebäude.

Ausnahmsweise können zugelassen werden

- die der Versorgung des Gebiets dienenden Läden, Schank- und Speisewirtschaften sowie nicht störende Handwerksbetriebe,
- Anlagen für kirchliche, kulturell, soziale, gesundheitliche und sportliche Zwecke,
- Betriebe des Beherbergungsgewerbes,
- sonstige nicht störende Gewerbebetriebe,
- Anlagen der Verwaltung.

Unzulässig und nicht Teil des Bebauungsplans sind

- Gartenbaubetriebe,
- Tankstellen.

(§ 9 Abs. 1 Nr. 1 BauGB i.V.m. §§ 4 und 1 Abs. 3, 5 und 6 BauNVO)

Maß der baulichen Nutzung

Höhe baulicher Anlagen

Unterer Bezugspunkt der maximal zulässigen Höhen baulicher Anlagen sind die in der Planzeichnung eingemessenen festgelegten Höhen über NHN im DHHN.

Oberer Bezugspunkt der maximal zulässigen Höhen baulicher Anlagen ist die Traufhöhe (TH).

Traufhöhe TH

Bezugspunkt ist der Schnittpunkt der Gebäudeaußenwand mit der Dachhaut.

Bauweise, überbaubare und nicht überbaubare Grundstücksfläche

Im Allgemeinen Wohngebiet ist eine Überschreitung der Baugrenze durch Terrassen um bis zu 3,00 m zulässig.

(§ 9 Abs. 1 Nr. 2 BauGB i.V.m. § 23 Abs. 3 BauNVO)

Mindestgröße für Baugrundstücke

Im Allgemeinen Wohngebiet müssen die Wohnbaugrundstücke eine Mindestgröße von 500 m² aufweisen.

(§ 9 Abs. 1 Nr. 3 BauGB)

Nebenanlagen und Stellplätze

Stellplätze, Garagen und Nebenanlagen i. S. d. § 14 BauNVO sind außerhalb der überbaubaren Grundstücksfläche zulässig.

(§ 9 Abs. 1 Nr. 4 und 22 BauGB i.V.m. § 23 Abs. 5 BauNVO)

Verkehrsflächen

Die Einteilung der Straßenverkehrsflächen ist nicht Gegenstand der Festsetzungen.

(§ 9 Abs. 1 Nr. 11 BauGB)

Mit Rechten zu belastende Flächen

Die Fläche mit der Bezeichnung GFLR ist mit einem Geh- und Fahrrecht zugunsten der Anlieger, mit einem Geh-, Fahr- und Leitungsrecht zugunsten der Ver- und Entsorgungsträger sowie einem Leitungsrecht zu Gunsten der Deutschen Telekom GmbH zu belasten.

(§ 9 Abs. 1 Nr. 21 BauGB)

Grünordnerische Festsetzungen

Im Allgemeinen Wohngebiet ist eine Befestigung von Stellplätzen und deren Zufahrten sowie von Wegen - ausgenommen in der Fläche mit der Bezeichnung GFLR - nur in wasser- und luftdurchlässigem Aufbau herzustellen (z.B. Großspflaster mit hohem Fugenanteil, wassergebundene Decke, Schotterterrassen, Rasengittersteine). Auch die Wasser- und Luftdurchlässigkeit wesentlich mindernde Befestigungen wie Betonunterbau, Fugenverguss, Asphaltierungen und Betonierungen sind unzulässig.

(§ 9 Abs. 1 Nr. 20 BauGB)

Örtliche Bauvorschriften

Im allgemeinen Wohngebiet sind die Dächer von Gebäuden als Sattel- oder Krüppelwalddächer mit Dachneigungen von mindestens 30 Grad auszuführen.

(§ 9 Abs. 4 BauGB i.V.m. § 87 Abs. 1 BbgBO)

Im Allgemeinen Wohngebiet sind Dacheindeckungen (z.B. Ziegel oder Dachsteine) nur in Rottönen zulässig.

(§ 9 Abs. 4 BauGB i.V.m. § 87 Abs. 1 BbgBO)

Im Geltungsbereich dieses Bebauungsplans ist die aktuelle Satzung über die Herstellung notwendiger Stellplätze in der Gemeinde Seddiner See (Stellplatzsatzung) vom 23.08.2005 (öffentlich bekannt gemacht am 12.12.2005) anzuwenden.

(§ 9 Abs. 4 BauGB i.V.m. § 87 Abs. 4 BbgBO)

Hinweise

Spezielle Artenschutzmaßnahmen

Vermeidungsmaßnahmen

- Bauzeitenregelung: Baufeldfreimachungen, Baustelleneinrichtungen, Gehölzbeseitigungen, Abbrucharbeiten sowie Gebäudesanierungsbeginn sind außerhalb der Fortpflanzungszeit, sprich im Zeitraum 01. Oktober bis 28. Februar, durchzuführen.
- Vor Gebäudeabbrüchen/-sanierungen sowie Fällungen von Höhlenbäumen sind die Gebäude hinsichtlich Niststätten von Gebäudebrutvögeln (nur wenn Bauarbeiten in der Brutzeit erfolgen) sowie auf sich möglicherweise im Jahresverlauf, in kleinen, schwer erkennbaren Quartierstrukturen aufhaltende einzelne Fledermäuse (gilt ganzjährig), durch eine nachweislich fachkundige Person zu kontrollieren. Beim Vorkommen von Brutvögeln und/oder Fledermäusen sind durch die fachkundige Person adäquate Schutz- und Kompensationsmaßnahmen zu ergreifen (Baustopp bis Ende Fortpflanzung bzw. bis zum Verlassen der Niststätten/Quartiere, ggf. Verbringung von Fledermäusen in Ersatzquartiere sowie Erhalt der Lebensstätten nach Baumaßnahme oder Anbringung von Ersatzniststätten/-quartieren vor Baumaßnahme).
- Die Beseitigung von Gehölzbeständen ist entsprechend § 39 BNatSchG nur außerhalb der Zeit 1. März bis 30. September zulässig. Sind Gehölzbeseitigungen innerhalb der Fortpflanzungs-/Vegetationszeiten unumgänglich, bedarf es einer Befreiung vom Verbot des § 39 BNatSchG sowie einer vorherigen Kontrolle bzgl. des Vorkommens geschützter Arten durch eine nachweislich fachkundige Person.

Vorgezogene Ausgleichsmaßnahmen

- Für den Verlust der 6 Lebensstätten von Feldsperling (1x), Kohlmeise (2x), Star (1x), Hausrotschwanz (1x) und Haussperling (1x) sind insgesamt 12 Ersatzniststätten (Feldsperling 2, Kohlmeise 4, Star 2, Hausrotschwanz 2, Haussperling 2) im ökologisch räumlichen Zusammenhang (an Gebäuden und Bäumen auf den das Plangebiet unmittelbar umgebenden Grundstücken) und für den zeitlichen Bezug, vor Beginn der auf den Verlust folgenden Brutperiode, also bis 28. Februar anzubringen.
- Für den Verlust der Lebensstätte der Rauchschnäbe (1x) sind insgesamt 4 Ersatzniststätten im ökologisch räumlichen Zusammenhang und für den zeitlichen Bezug, vor Beginn der auf den Verlust folgenden Brutperiode, also bis 28. Februar an/in Gebäuden anzubringen.

Telekommunikationsversorgung

In allen Straßen bzw. Gehwegen sind geeignete und ausreichende Trassen mit einer Leitungszone in einer Breite von ca. 0,5 m für die Unterbringung der Telekommunikationslinien der Telekom vorzusehen.

Hinsichtlich geplanter Baumpflanzungen ist das "Merkblatt über Baumstandorte und unterirdische Ver- und Entsorgungsanlagen" der Forschungsgesellschaft für Straßen- und Verkehrswesen, Ausgabe 1989 zu beachten.

Baumpflanzungen

Bei Baumpflanzungen ist ohne Sicherungsmaßnahmen ein Abstand zu Leitungen von mindestens 2,5 m von der Rohraußenkante und Stromkabel zu den Stammachsen einzuhalten. Bei Unterschreitung dieses Abstandes sind in Abstimmung mit der NBB Schutzmaßnahmen festzulegen. Ein Mindestabstand von 1,5 m sollte jedoch in allen Fällen angestrebt werden. Bei Unterschreitung dieses Abstandes sind nur flach wurzelnde Bäume einzupflanzen, wobei gesichert werden muss, dass beim Herstellen der Pflanzgrube der senkrechte Abstand zwischen Sohle Pflanzgrube und Oberkante unserer Leitungen und Kabel mindestens 0,3 m beträgt. Weiter ist zwischen Rohrleitung/Kabel und zu dem pflanzenden Baum eine PVC-Baumenschutzplatte einzubringen.

Wasserrechtliche Erlaubnis

Sofern das Niederschlagswasser gesammelt und über unterirdische Versickerungsanlagen (z.B. Rigolen, Sickerschächte) ins Grundwasser abgeleitet werden soll, ist mit dem Antrag auf Baugenehmigung eine wasserrechtliche Erlaubnis nach § 8 Abs. 1 des Wasserhaushaltsgesetzes bei der Unteren Wasserbehörde des Landkreises Potsdam-Mittelmark zu beantragen.

Gemeinde Seddiner See

Bebauungsplan "Neues Wohnen am Fischerhof"

Gemarkung Seddiner Flur 2, Flst. 643
Gemarkung Kähnsdorf Flur 1, Flst. 247, 535, 536, 537

Satzungsexemplar

Stand: 02.03.2021
Maßstab: 1:1000 auf A2

Auftraggeber:
Gemeinde
Seddiner See
Kiefernweg 5
14554 Seddiner See

Auftragnehmer:
Jahn, Mack & Partner
architektur und stadtplanung mbB
Wilhelm-Kabus-Straße 74
10829 Berlin

Plangrundlage (Stand: 02/2020):
ÖbVI Eberhard Schmidt, 14554 Seddiner See
Höhenbezug DHHN2016
Lagesystem ETRS 89

JAHN, MACK & PARTNER
architektur und stadtplanung mbB